

Проект реконструкції приміщення
вул. Маркіяна Шашкевича, 9, А-2
м. Золочів

Арк	Найменування	Масштаб
2	Обмірний план	1 : 50
3	План монтажу г/к перегородок	1 : 50
4	План заповнення дверних отворів	1 : 50
5	План опорядження стін	1 : 50
6	План розміщення вимикачів і точок освітлення	1 : 50
7	План розміщення меблів та обладнання	1 : 50

www.behance.net/natalia_pyndyk

+380 967 638 994 - Наталя Пиндик

ПРОЕКТ

ПРОЕКТ
РЕКОНСТРУКЦІЇ
ПРИМІЩЕННЯ

вул. М. Шашкевича, 9
А-2, м. Золочів

НАЗВА АРКУША:

ОБМІРНИЙ ПЛАН

ДАТА: 12.03.2025

ПРОЕКТ №:


СТАДІЯ РП

ДИЗАЙН:
ПИНДИК НАТАЛЯ

КРЕСЛИВ:
ПИНДИК НАТАЛЯ

МАСШТАБ 1:75

ФОРМАТ ЛИСТА А3

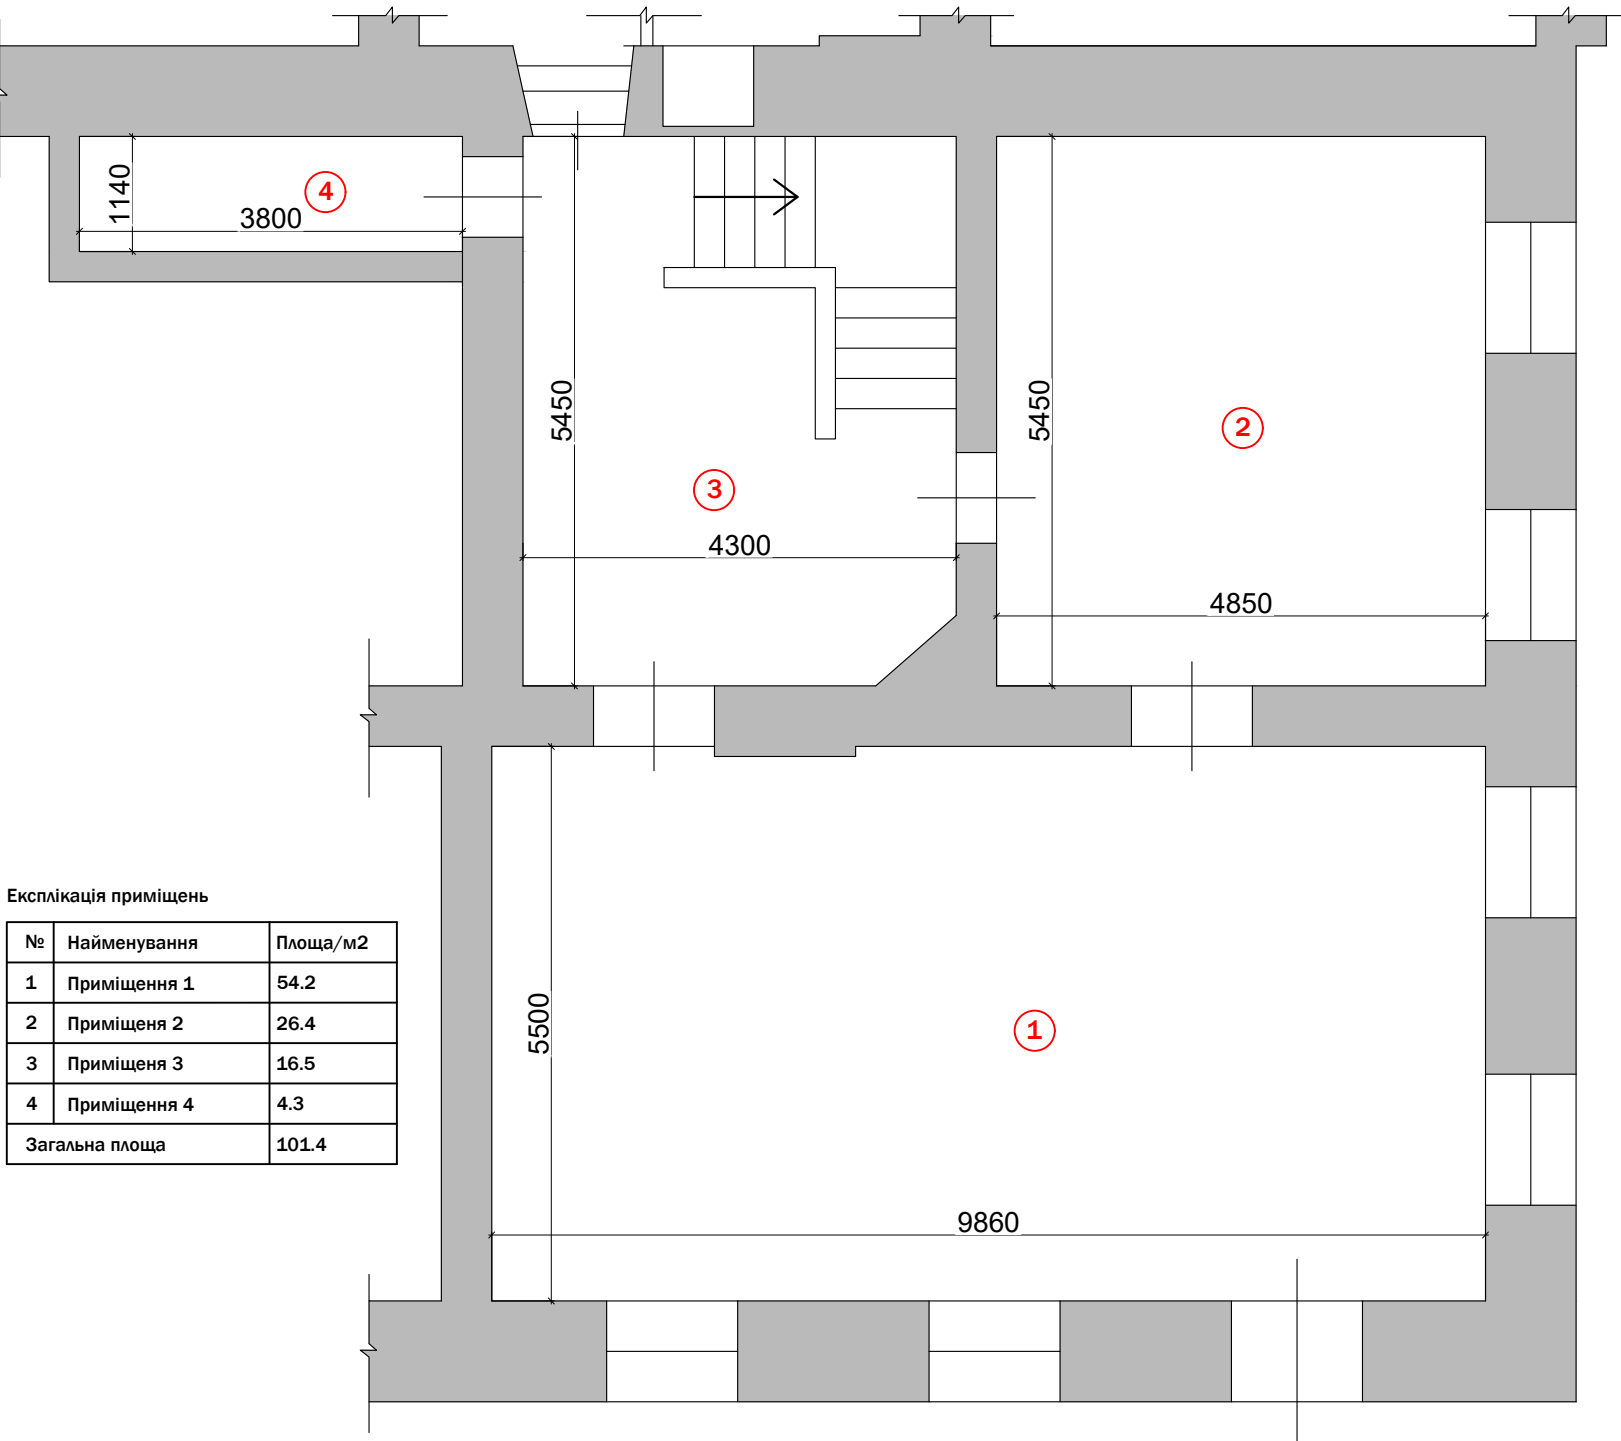

www.behance.net/natalia_pyndyk

+380 967 638 994 - Наталя Пиндик

ПРОЄКТ

ПРОЄКТ
РЕКОНСТРУКЦІЇ
ПРИМІЩЕННЯ

вул. М. Шашкевича, 9
А-2, м. Золочів

НАЗВА АРКУША:

ПЛАН МОНТАЖУ
Г/К ПЕРЕГОРОДОК

ДАТА: 12.03.2025

ПРОЄКТ №:


СТАДІЯ РП

ДИЗАЙН:
ПИНДИК НАТАЛЯ

КРЕСЛИВ:
ПИНДИК НАТАЛЯ

МАСШТАБ 1:75

ФОРМАТ ЛИСТА А3

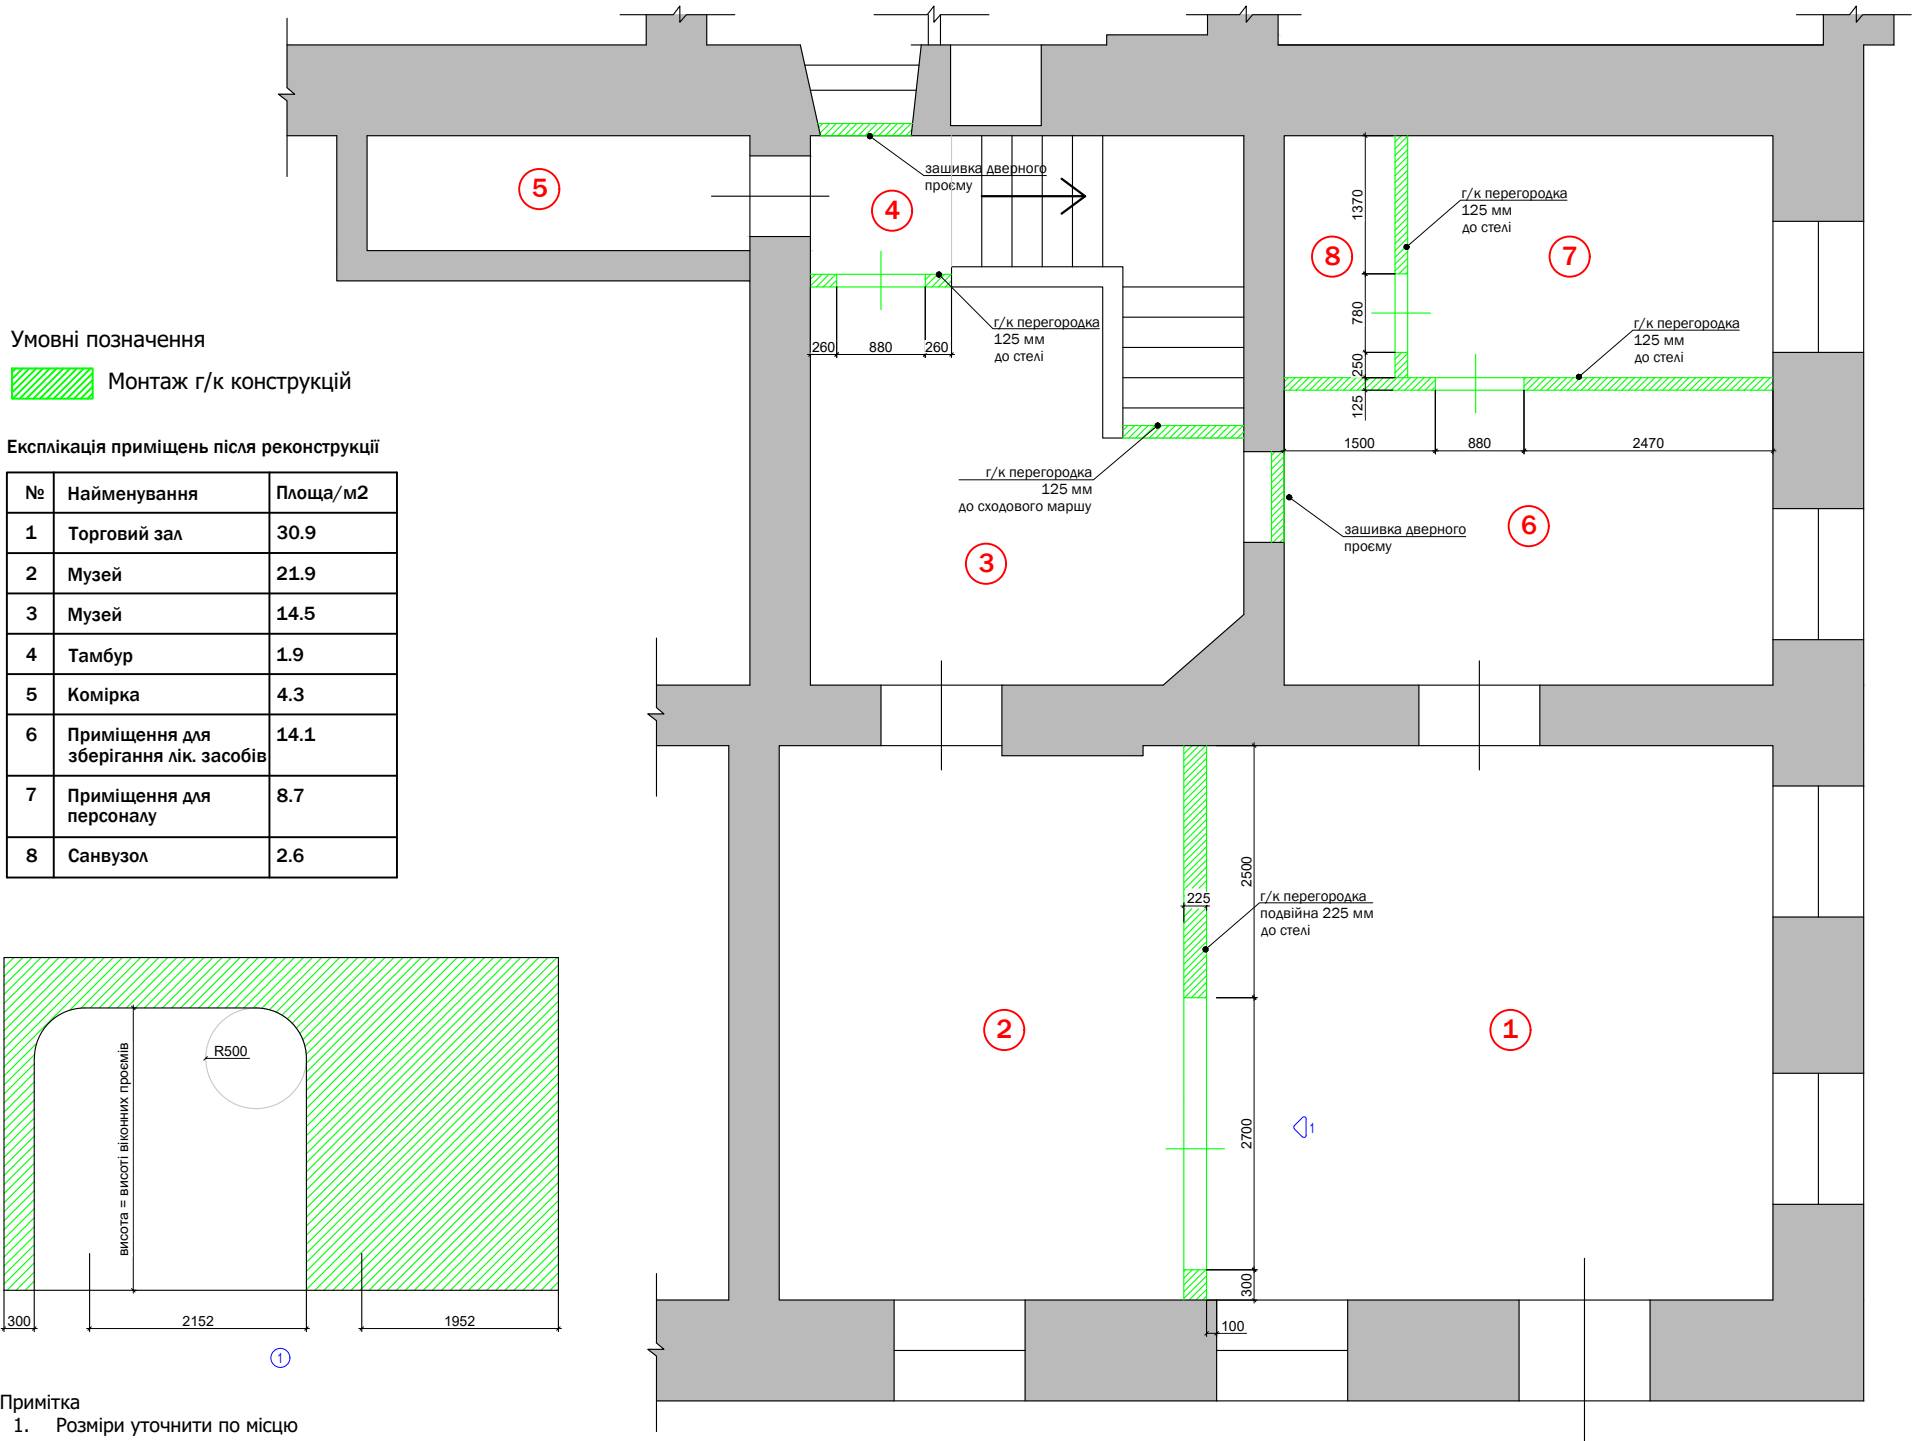

www.behance.net/natalia_pyndyk

+380 967 638 994 - Наталя Пиндик

ПРОЄКТ

ПРОЄКТ
РЕКОНСТРУКЦІЇ
ПРИМІЩЕННЯ

вул. М. Шашкевича, 9
А-2, м. Золочів

НАЗВА АРКУША:

ПЛАН
ЗАПОВНЕННЯ
ДАЕРНИХ ОТВОРІВ

ДАТА: 12.03.2025

ПРОЄКТ №:


СТАДІЯ РП

ДИЗАЙН:
ПИНДИК НАТАЛЯ

КРЕСЛИВ:
ПИНДИК НАТАЛЯ

МАСШТАБ 1:75

ФОРМАТ ЛИСТА А3

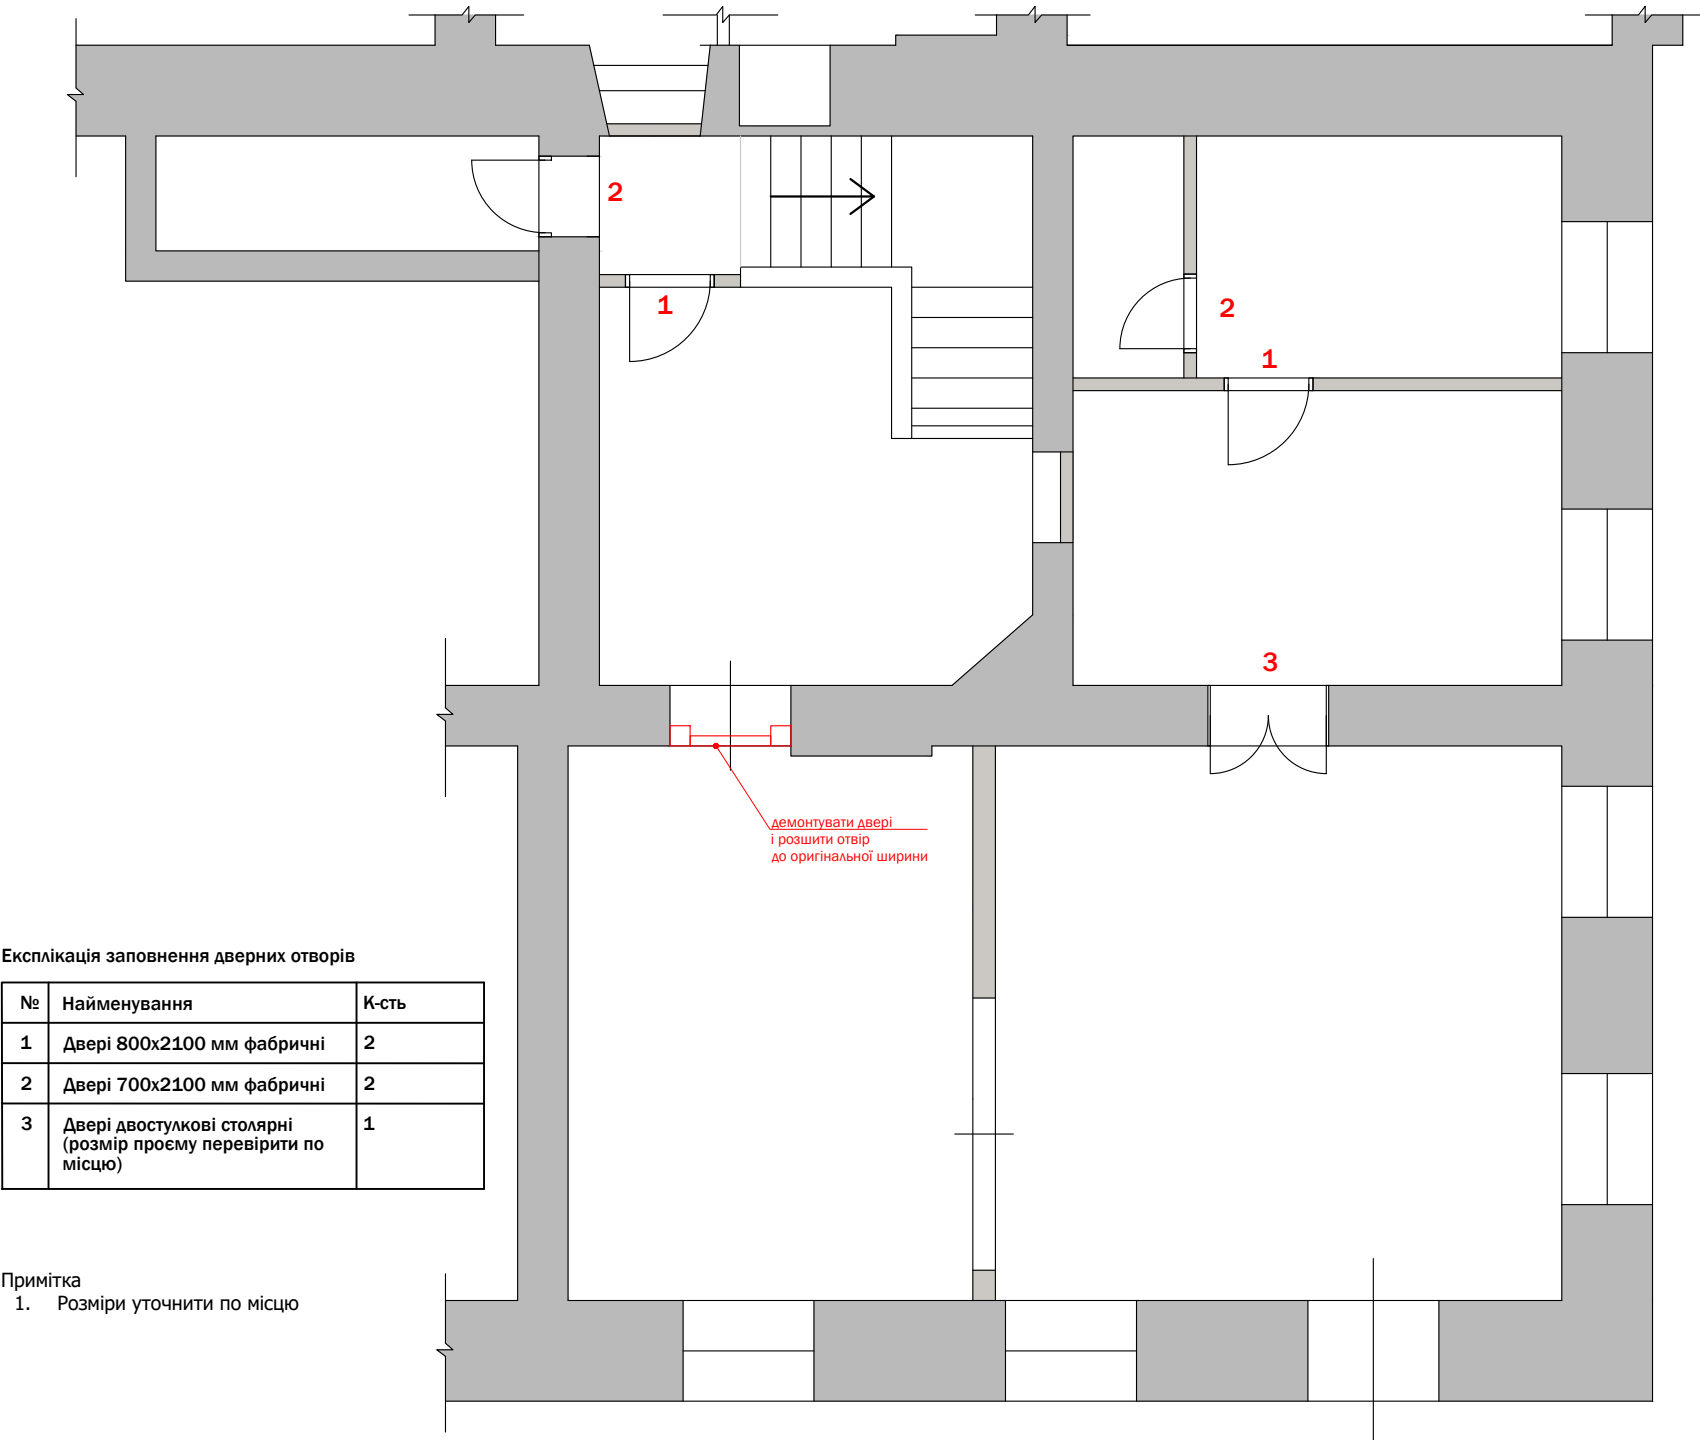

Експлікація заповнення дверних отворів

№	Найменування	К-сть
1	Двері 800х2100 мм фабричні	2
2	Двері 700х2100 мм фабричні	2
3	Двері двостулкові столярні (розмір проєму перевірити по місцю)	1

Примітка

1. Розміри уточнити по місцю

www.behance.net/natalia_pyndyk

+380 967 638 994 - Наталя Пиндик

ПРОЕКТ

ПРОЕКТ
РЕКОНСТРУКЦІЇ
ПРИМІЩЕННЯ

вул. М. Шашкевича, 9
А-2, м. Золочів

НАЗВА АРКУША:

ПЛАН
ОПОРЯДЖЕННЯ
СТІН

ДАТА:12.03.2025

ПРОЕКТ №:


СТАДІЯРП

ДИЗАЙН:
ПИНДИК НАТАЛЯ

КРЕСЛИВ:
ПИНДИК НАТАЛЯ

МАСШТАБ1:75

ФОРМАТ ЛИСТАА3

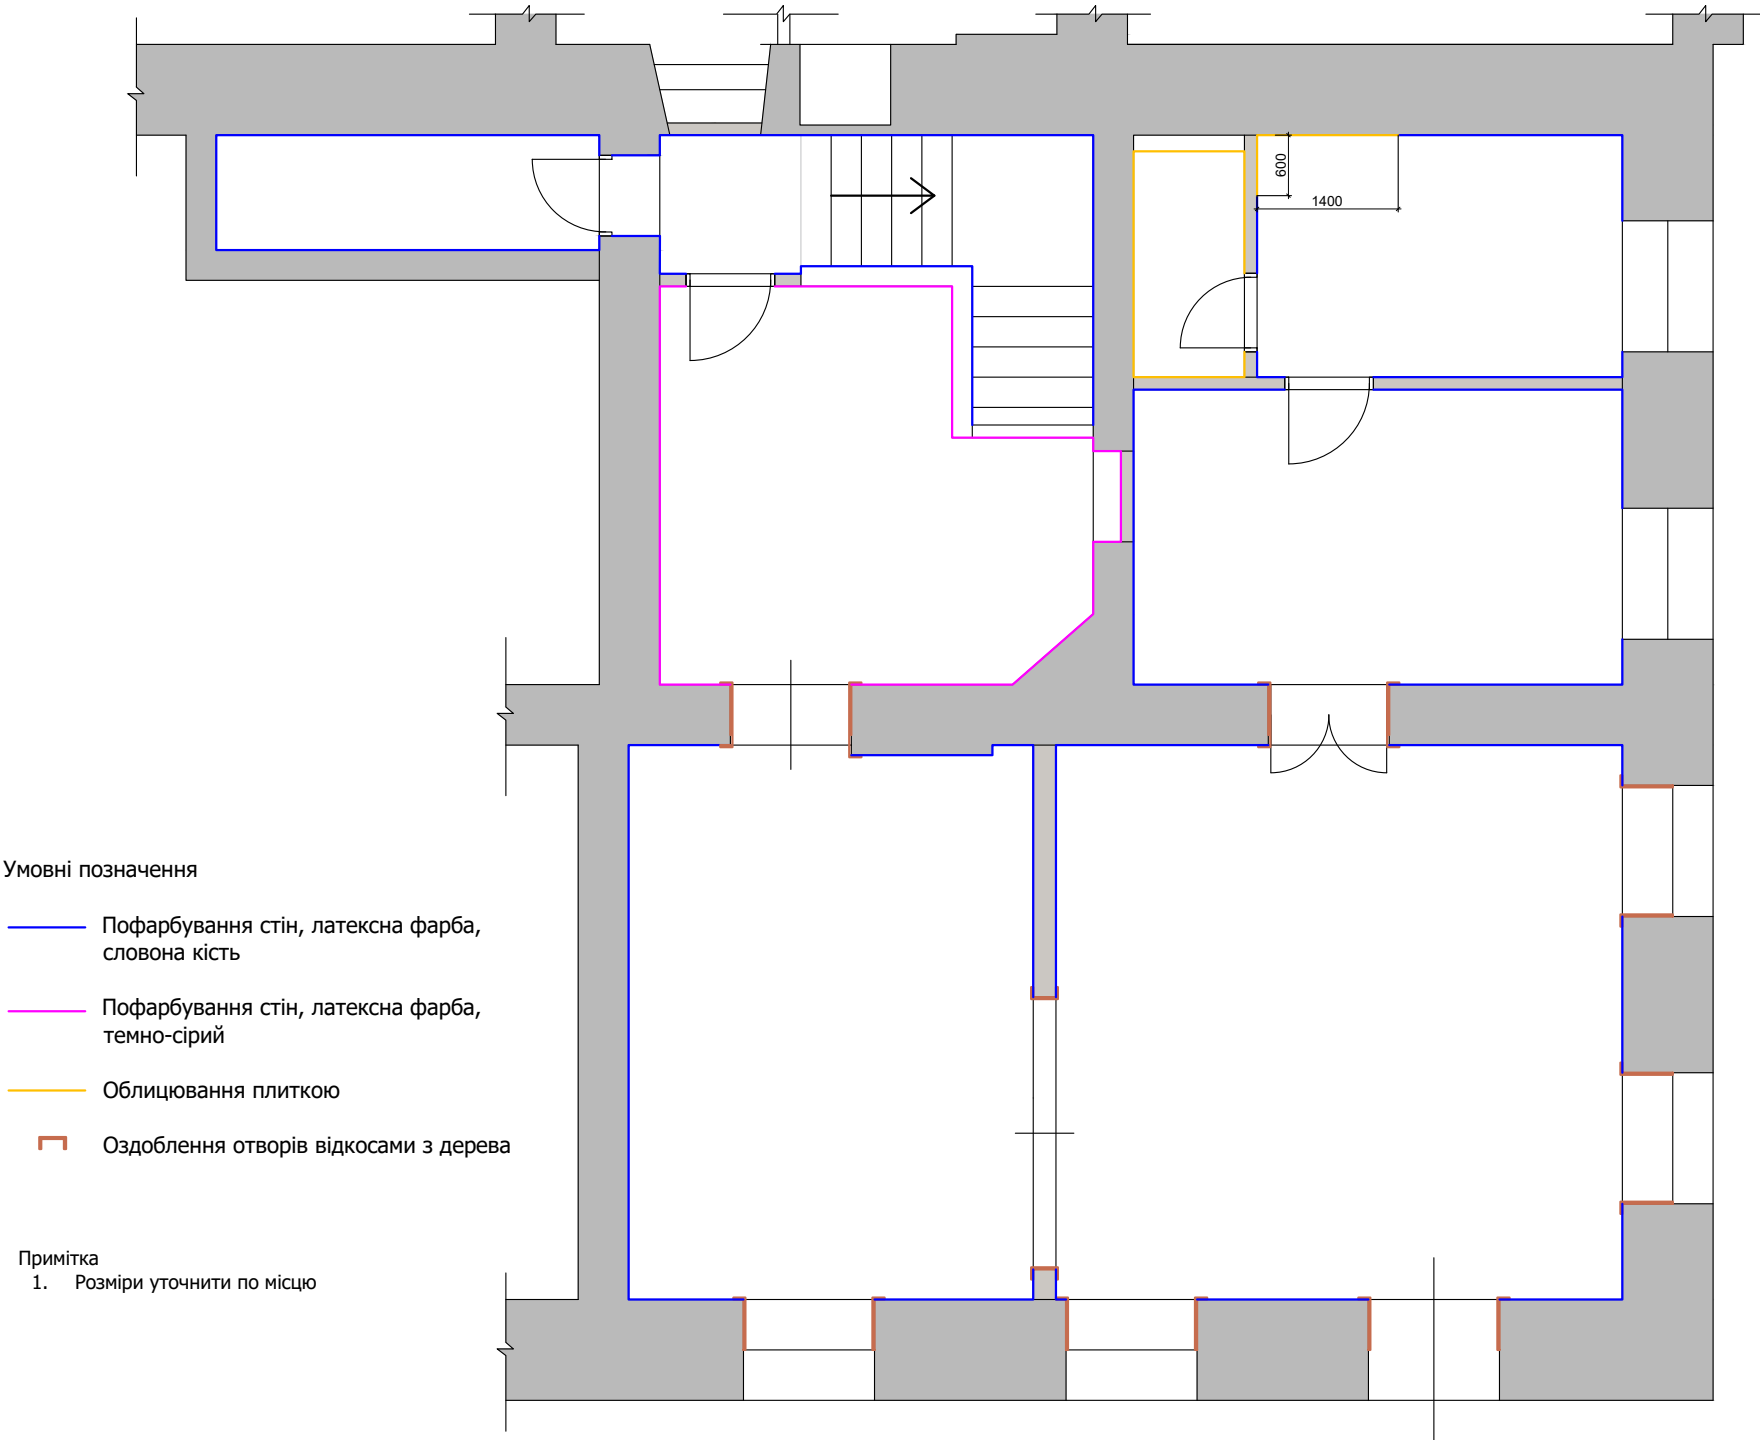

www.behance.net/natalia_pyndyk

+380 967 638 994 - Наталя Пиндик

ПРОЕКТ

ПРОЕКТ
РЕКОНСТРУКЦІЇ
ПРИМІЩЕННЯ

вул. М. Шашкевича, 9
А-2, м. Золочів

НАЗВА АРКУША:

ПЛАН
РОЗМІЩЕННЯ
ТОЧОК
ОСВІТЛЕННЯ

ДАТА: 12.03.2025

ПРОЕКТ №:


СТАДІЯ РП

ДИЗАЙН:
ПИНДИК НАТАЛЯ

КРЕСЛИВ:
ПИНДИК НАТАЛЯ

МАСШТАБ 1:75

ФОРМАТ ЛИСТА А3

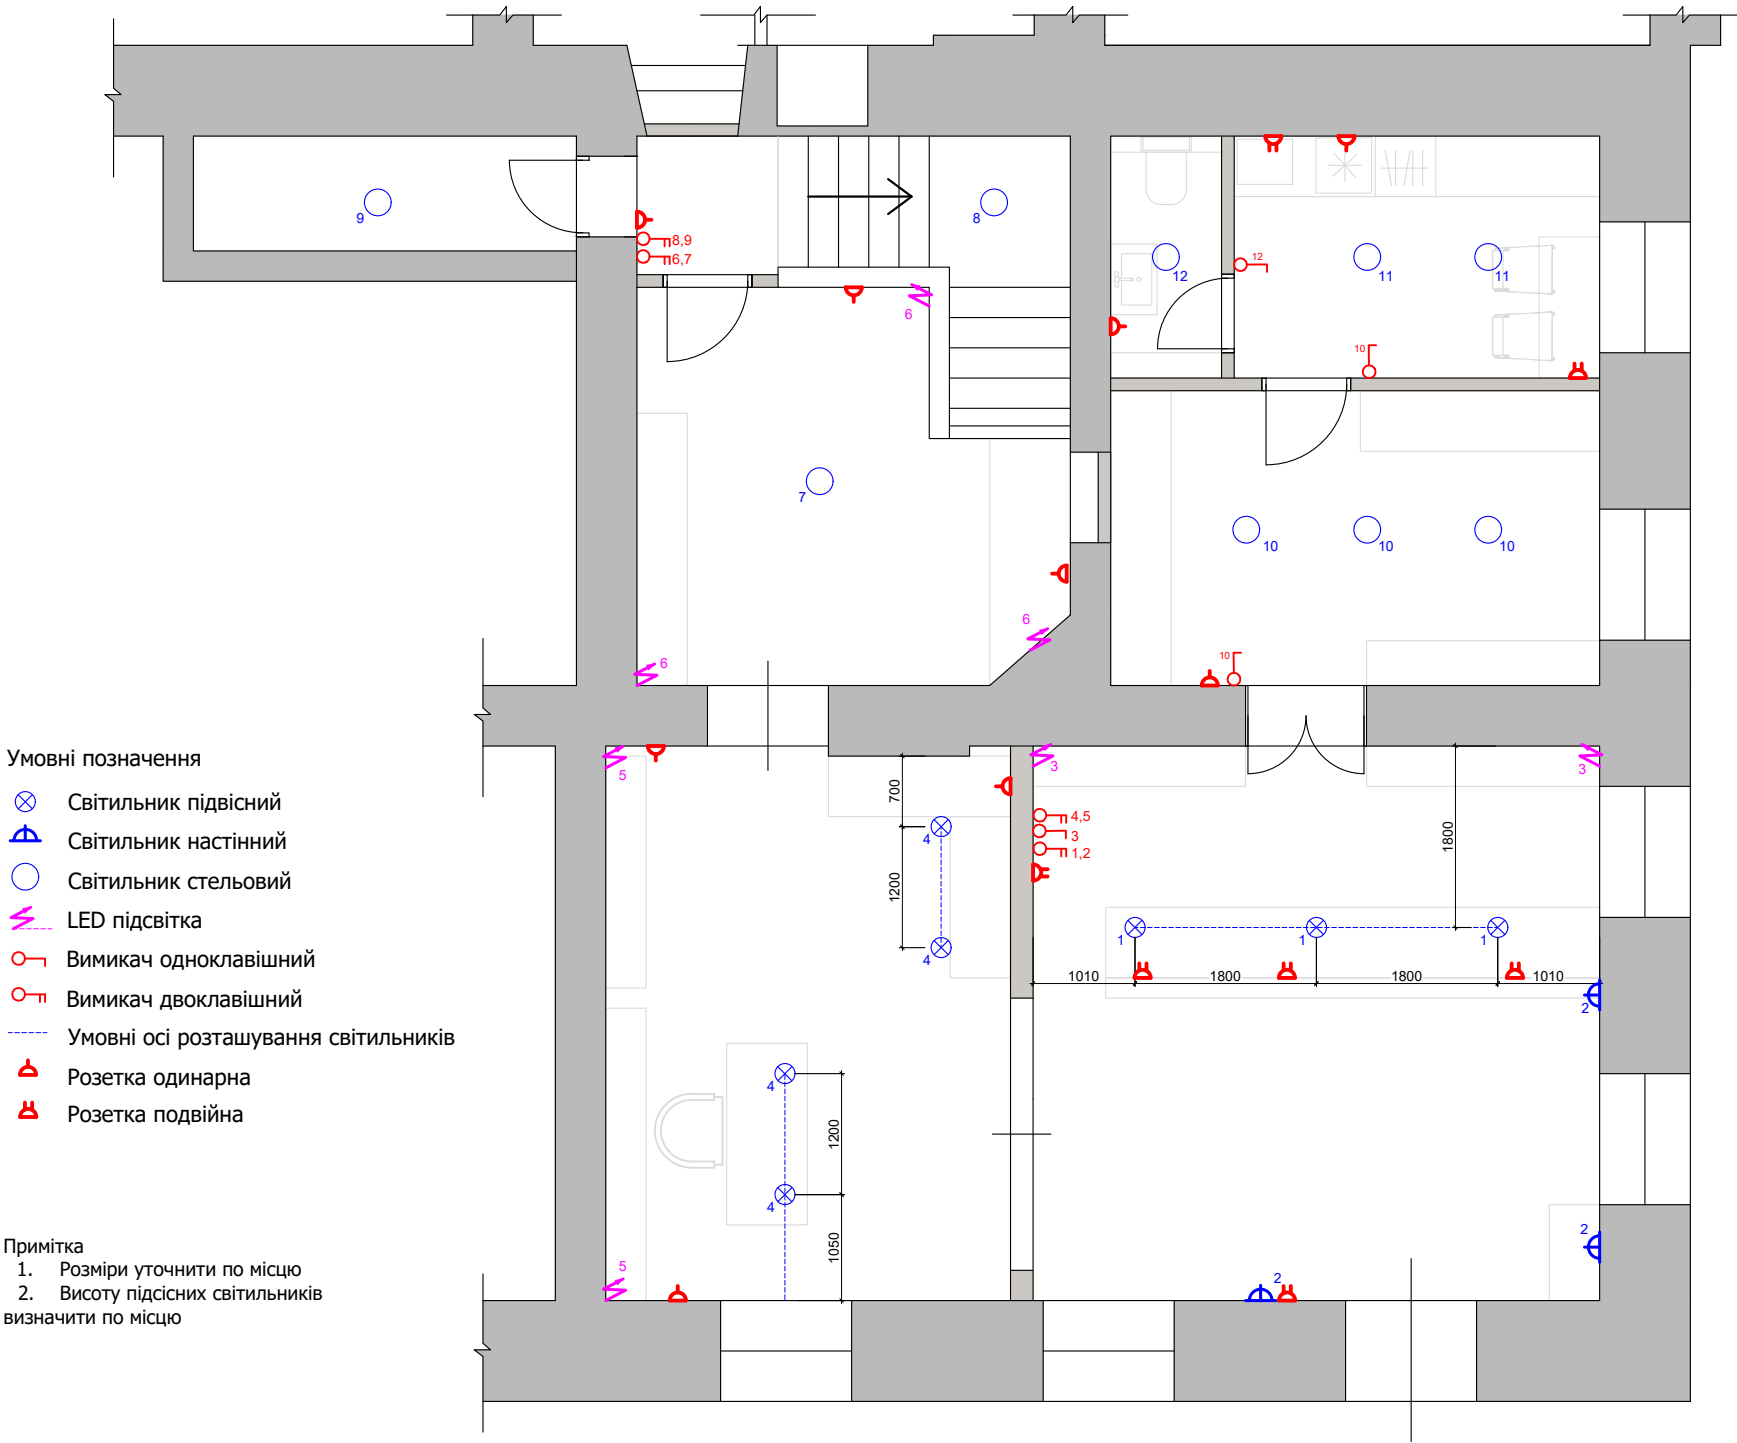

www.behance.net/natalia_pyndyk

+380 967 638 994 - Наталя Пиндик

ПРОЕКТ

ПРОЕКТ
РЕКОНСТРУКЦІЇ
ПРИМІЩЕННЯ

вул. М. Шашкевича, 9
А-2, м. Золочів

НАЗВА АРКУША:

ПЛАН
РОЗМІЩЕННЯ
ОБЛАДНАННЯ

ДАТА: 12.03.2025

ПРОЕКТ №:

СТАДІЯ РП

ДИЗАЙН:
ПИНДИК НАТАЛЯ

КРЕСЛИВ:
ПИНДИК НАТАЛЯ

МАСШТАБ 1:75

ФОРМАТ ЛИСТА А3

