

Проект реконструкції приміщення
вул. Маркіяна Шашкевича, 9, А-2
м. Золочів

Арк	Найменування	Масштаб
2	Обмірний план	1 : 75
3	План монтажу г/к перегородок	1 : 75
4	План заповнення дверних отворів	1 : 75
5	План опорядження стін	1 : 75
6	План розміщення вимикачів і точок освітлення	1 : 75
7	План розміщення обладнання	1 : 75
8	Креслення обладнання під виготовлення	1 : 50

www.behance.net/natalia_pyndyk

+380 967 638 994 - Наталя Пиндик

ПРОЕКТ

ПРОЕКТ
РЕКОНСТРУКЦІЇ
ПРИМІЩЕННЯ

вул. М. Шашкевича, 9
А-2, м. Золочів

НАЗВА АРКУША:

ОБМІРНИЙ ПЛАН

ДАТА: 12.03.2025

ПРОЕКТ №: РП


СТАДІЯ

ДИЗАЙН:
ПИНДИК НАТАЛЯ

КРЕСЛИВ:
ПИНДИК НАТАЛЯ

МАСШТАБ 1:75

ФОРМАТ ЛИСТА А3

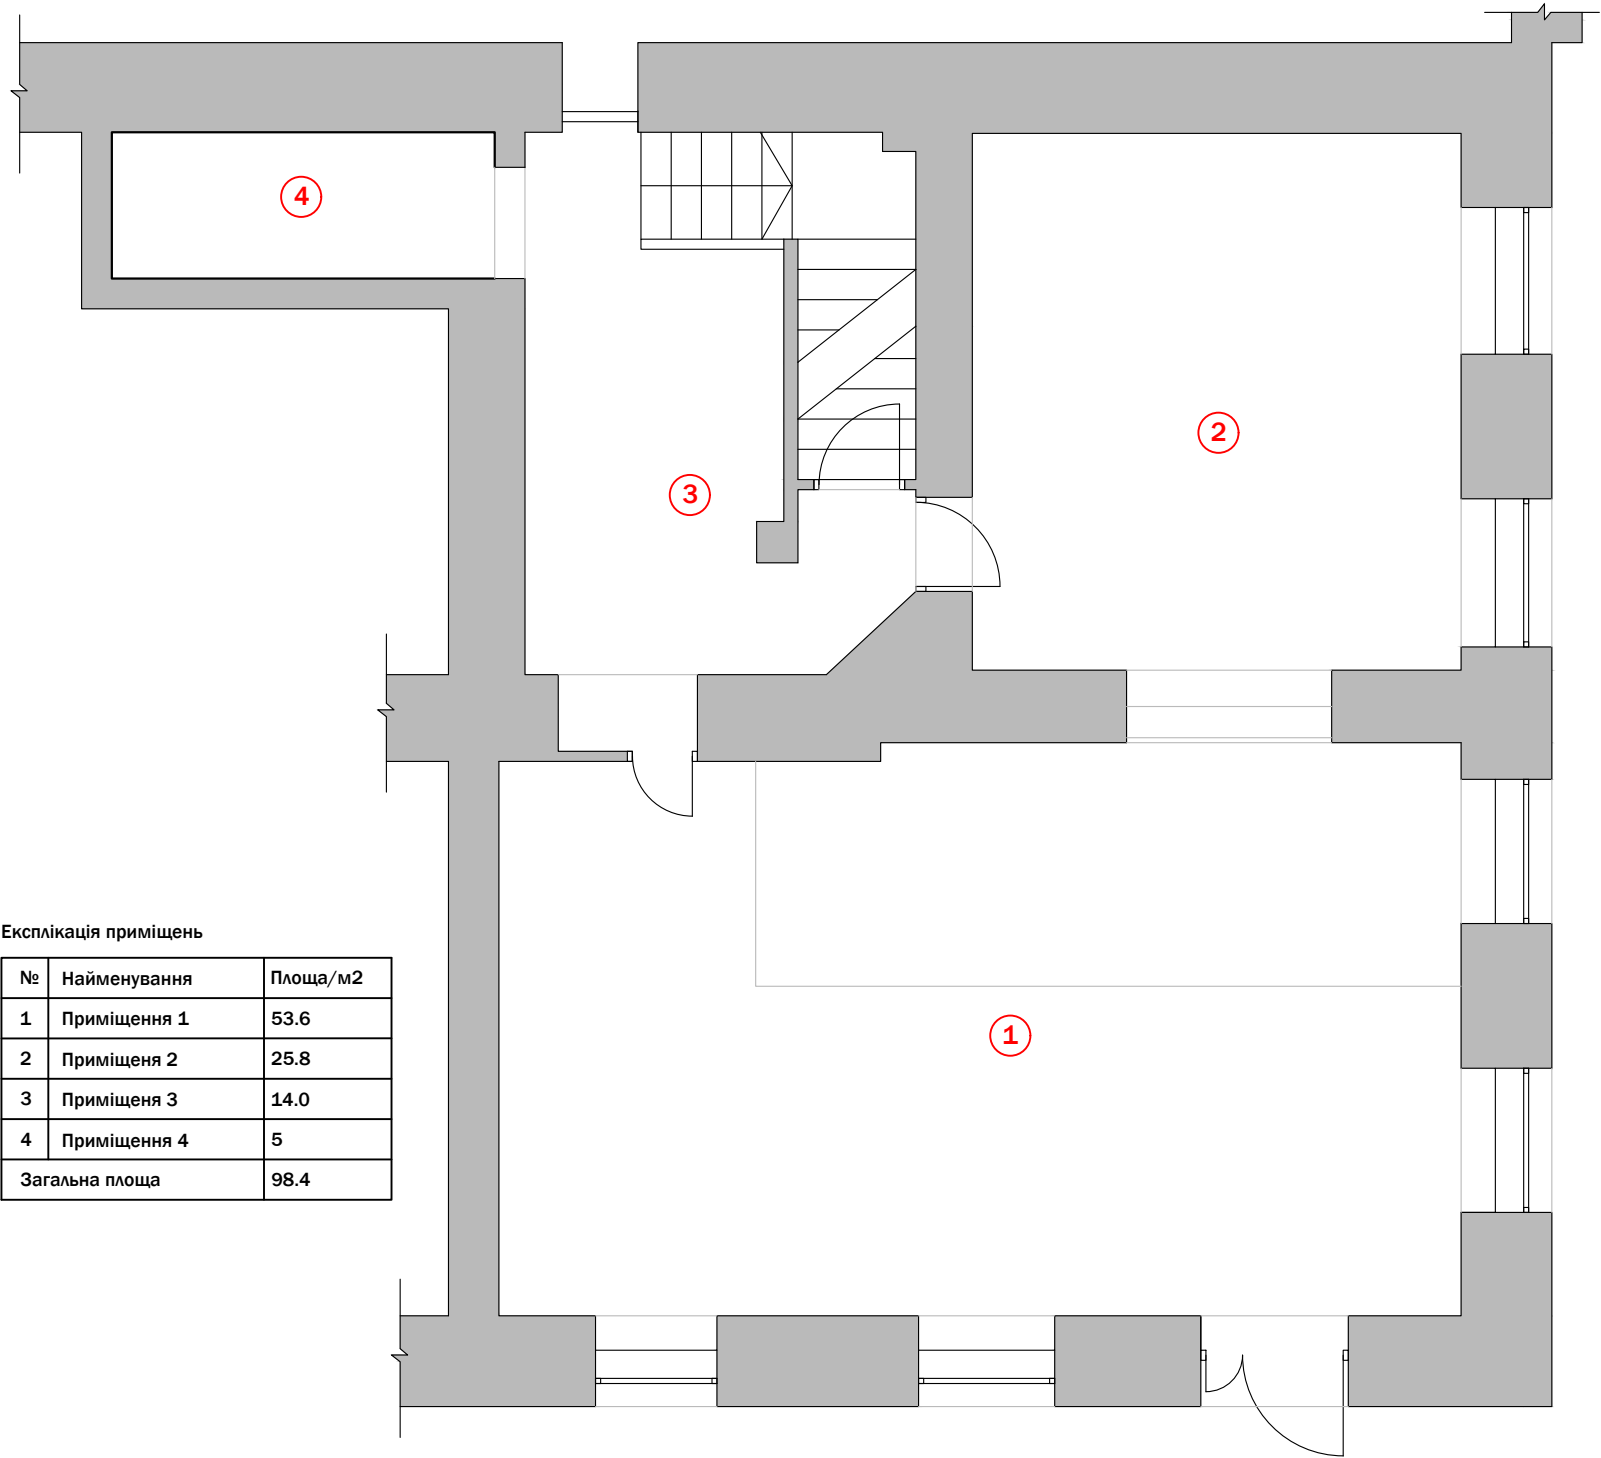

www.behance.net/natalia_pyndyk

+380 967 638 994 - Наталя Пиндик

ПРОЕКТ

ПРОЕКТ
РЕКОНСТРУКЦІЇ
ПРИМІЩЕННЯ

вул. М. Шашкевича, 9
А-2, м. Золочів

НАЗВА АРКУША:


ПЛАН
ДЕМОНТАЖУ
КОНСТРУКЦІЙ

ДАТА:	12.03.2025
ПРОЕКТ №:	
СТАДІЯ	РП

ДИЗАЙН:
ПИНДИК НАТАЛЯ

КРЕСЛИВ:
ПИНДИК НАТАЛЯ

МАСШТАБ	1:75
ФОРМАТ ЛИСТА	A3

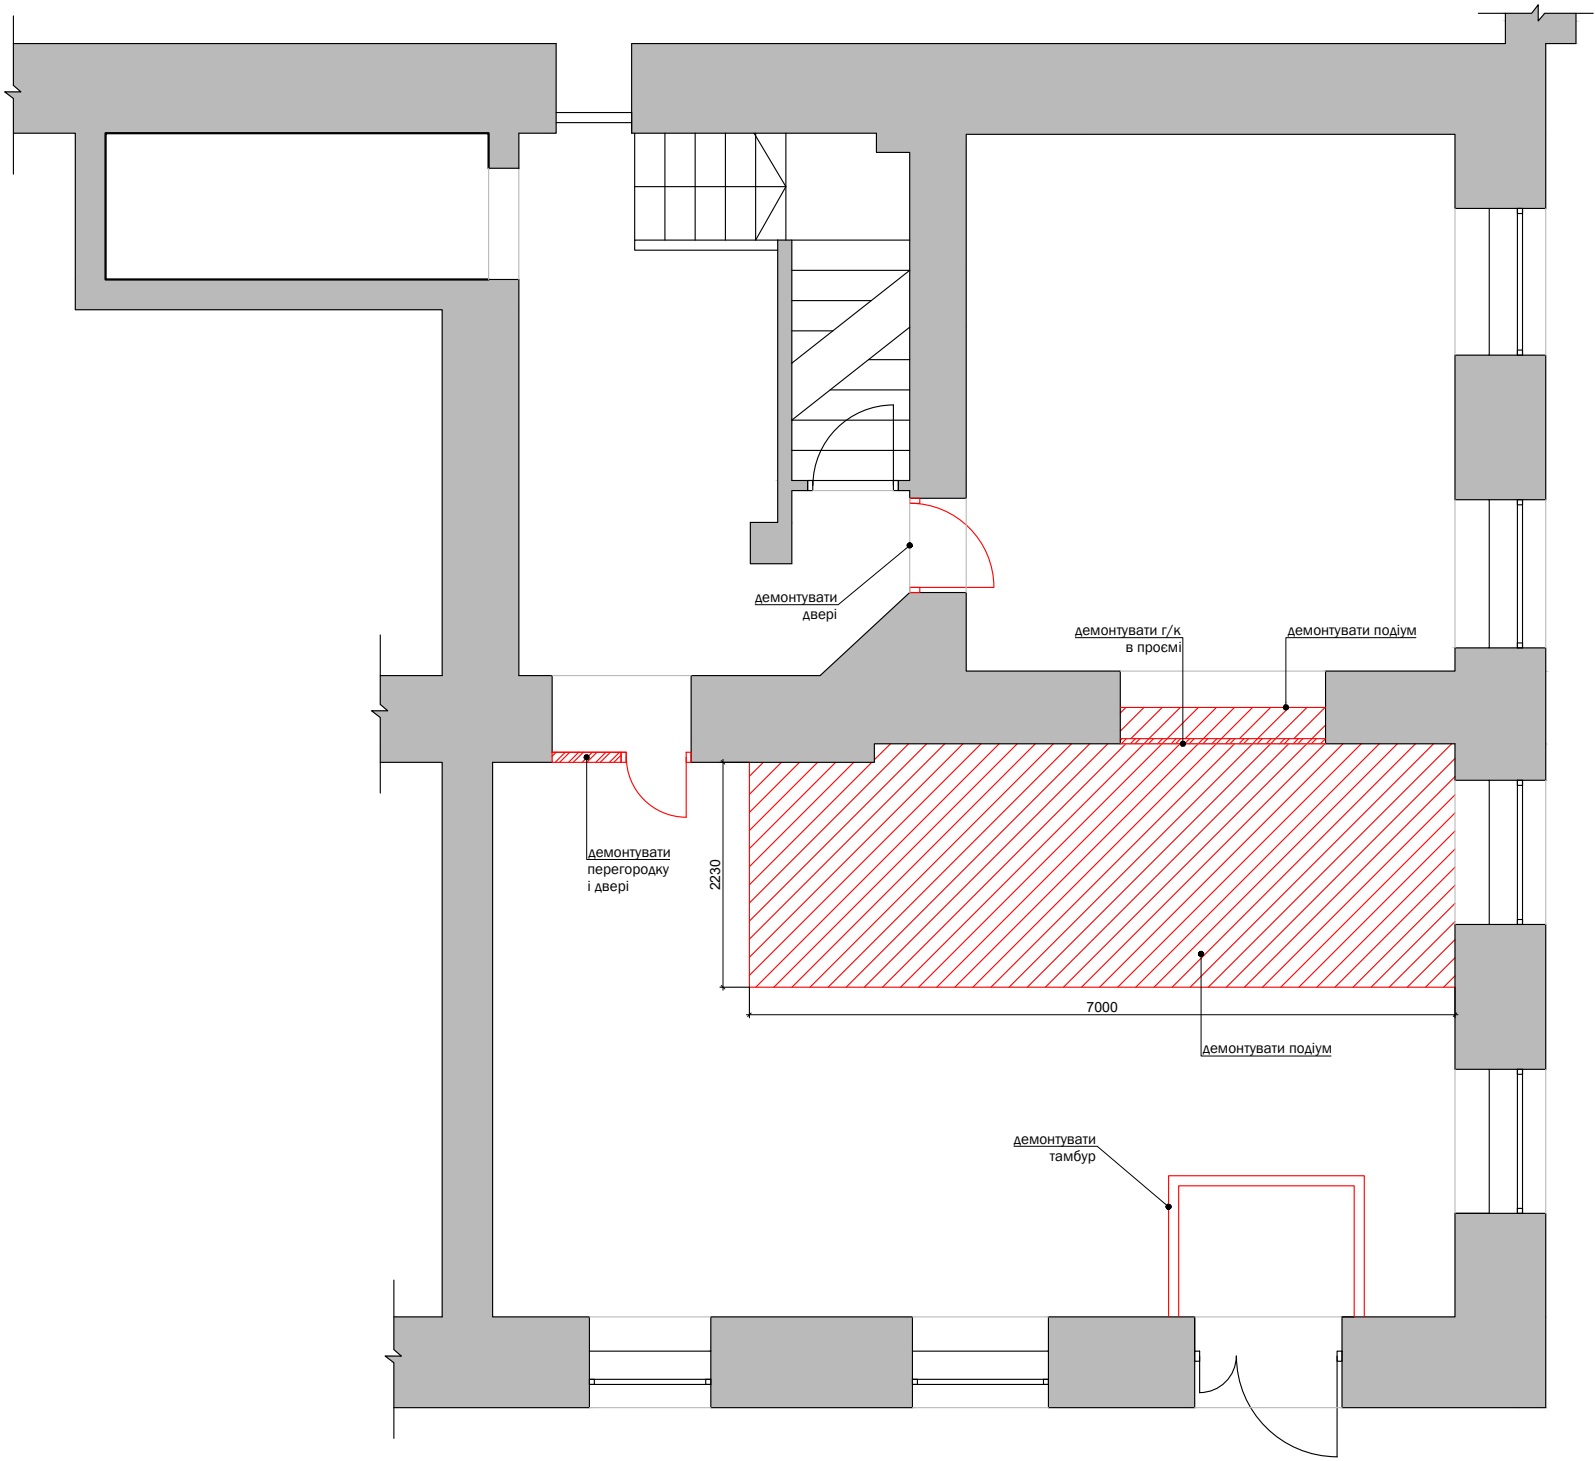

www.behance.net/natalia_pyndyk

+380 967 638 994 - Наталя Пиндик

ПРОЕКТ

ПРОЕКТ
РЕКОНСТРУКЦІЇ
ПРИМІЩЕННЯ

вул. М. Шашкевича, 9
А-2, м. Золочів

НАЗВА АРКУША:

ПЛАН МОНТАЖУ
Г/К КОНСТРУКЦІЙ
І ЗАПОВНЕННЯ
ДВЕРНИХ ОТВОРІВ

ДАТА: 12.03.2025

ПРОЕКТ №:


СТАДІЯ РП

ДИЗАЙН:
ПИНДИК НАТАЛЯ

КРЕСЛИВ:
ПИНДИК НАТАЛЯ

МАСШТАБ 1:75

ФОРМАТ ЛИСТА А3

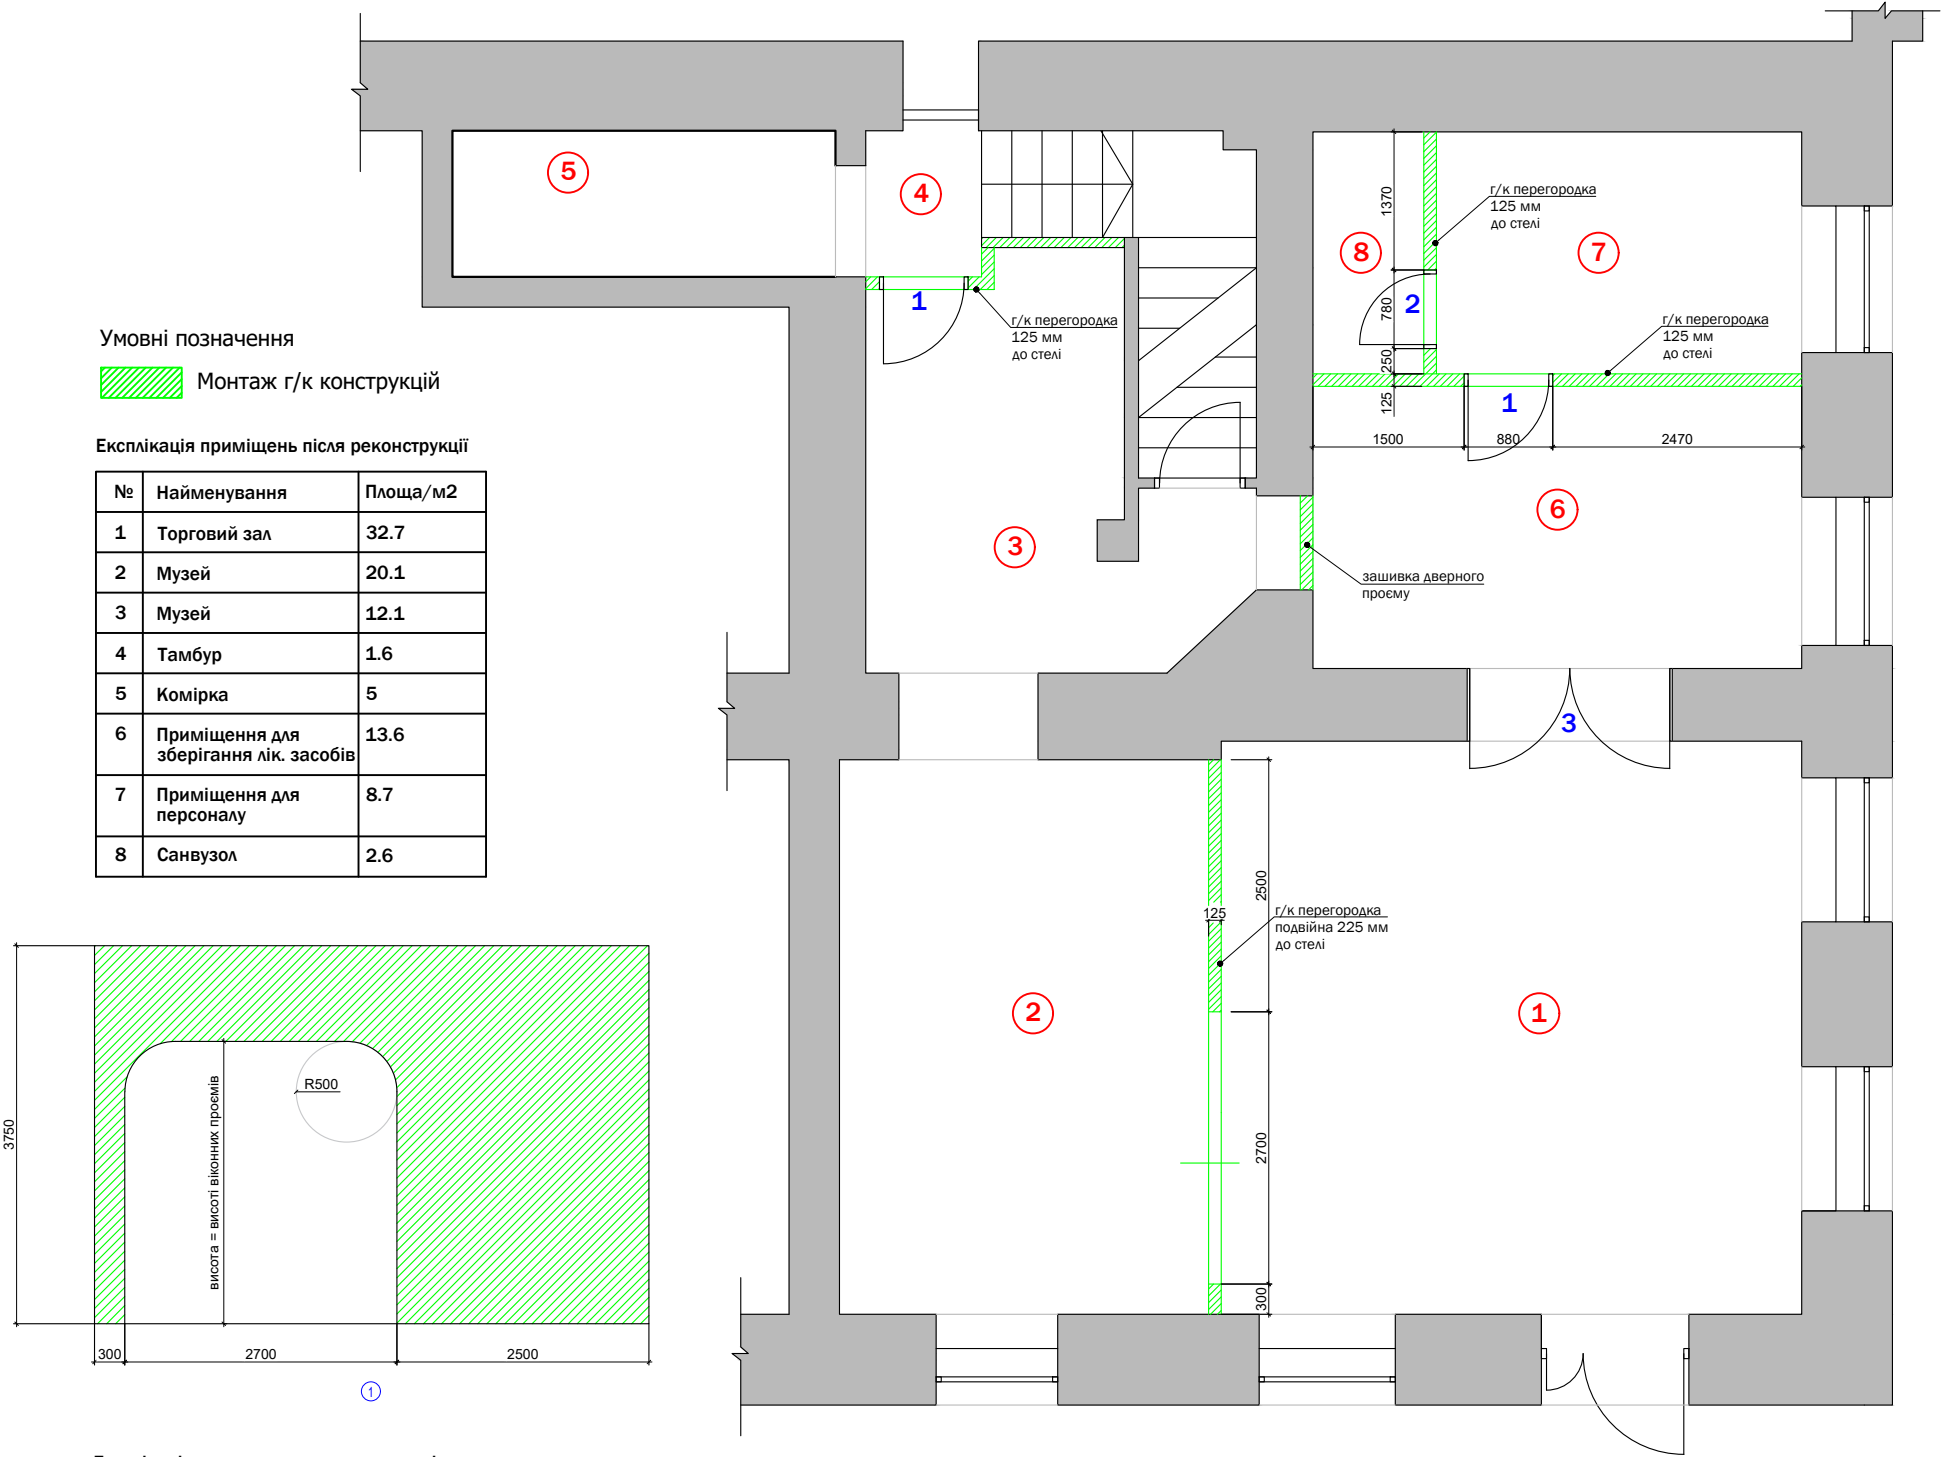

www.behance.net/natalia_pyndyk

+380 967 638 994 - Наталя Пиндик

ПРОЄКТ

ПРОЄКТ
РЕКОНСТРУКЦІЇ
ПРИМІЩЕННЯ

вул. М. Шашкевича, 9
А-2, м. Золочів

НАЗВА АРКУША:

ПЛАН
ОПОРЯДЖЕННЯ
СТІН

ДАТА: 12.03.2025

ПРОЄКТ №:


СТАДІЯ РП

ДИЗАЙН:
ПИНДИК НАТАЛЯ

КРЕСЛИВ:
ПИНДИК НАТАЛЯ

МАСШТАБ 1:75

ФОРМАТ ЛИСТА А3

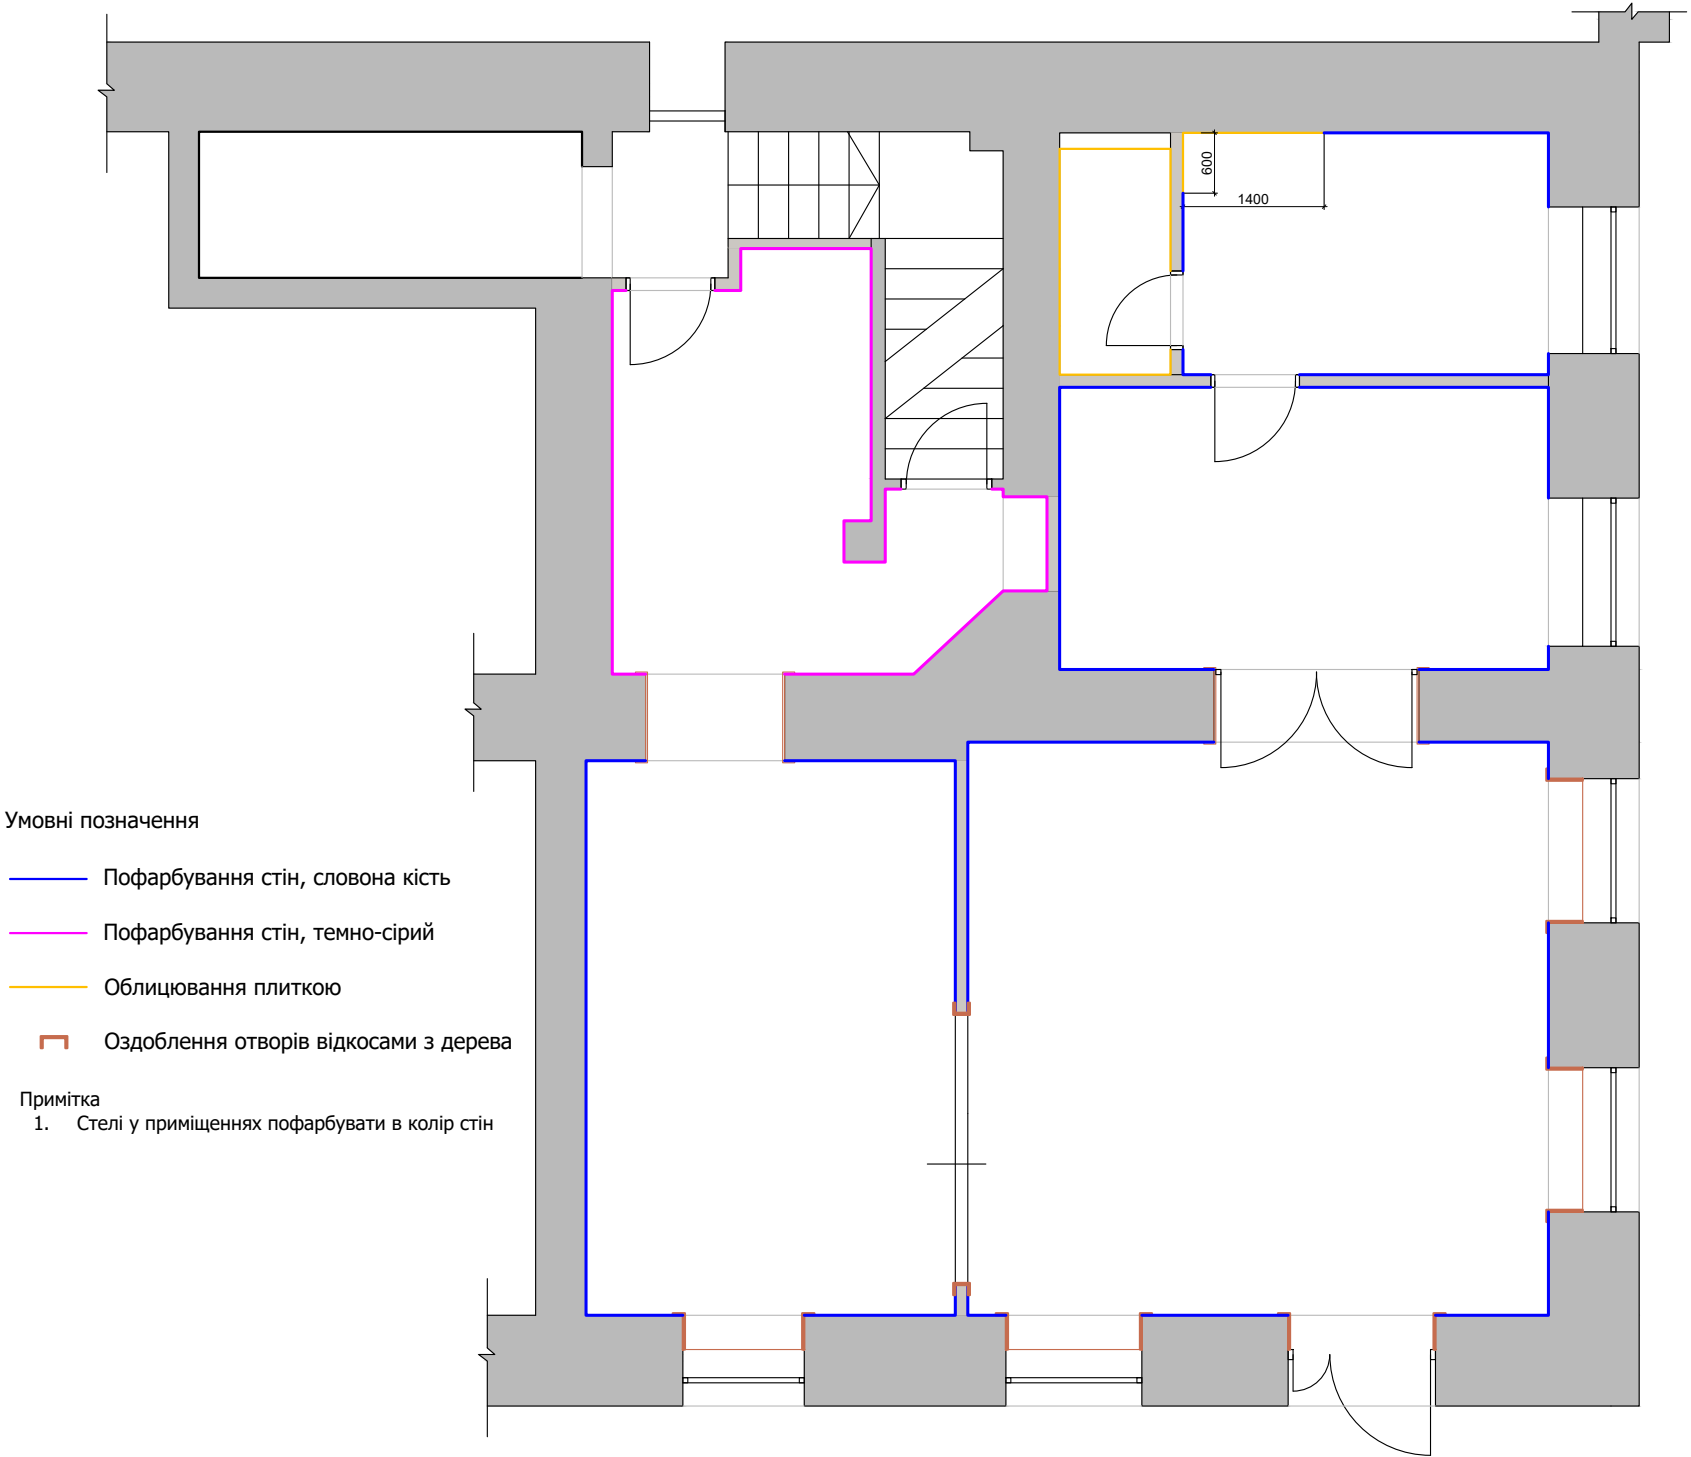

www.behance.net/natalia_pyndyk

+380 967 638 994 - Наталя Пиндик

ПРОЕКТ

ПРОЕКТ
РЕКОНСТРУКЦІЇ
ПРИМІЩЕННЯ

вул. М. Шашкевича, 9
А-2, м. Золочів

НАЗВА АРКУША:

ПЛАН
РОЗМІЩЕННЯ
ТОЧОК
ОСВІТЛЕННЯ

ДАТА: 12.03.2025

ПРОЕКТ №:


СТАДІЯ РП

ДИЗАЙН:
ПИНДИК НАТАЛЯ

КРЕСЛИВ:
ПИНДИК НАТАЛЯ

МАСШТАБ 1:75

ФОРМАТ ЛИСТА А3

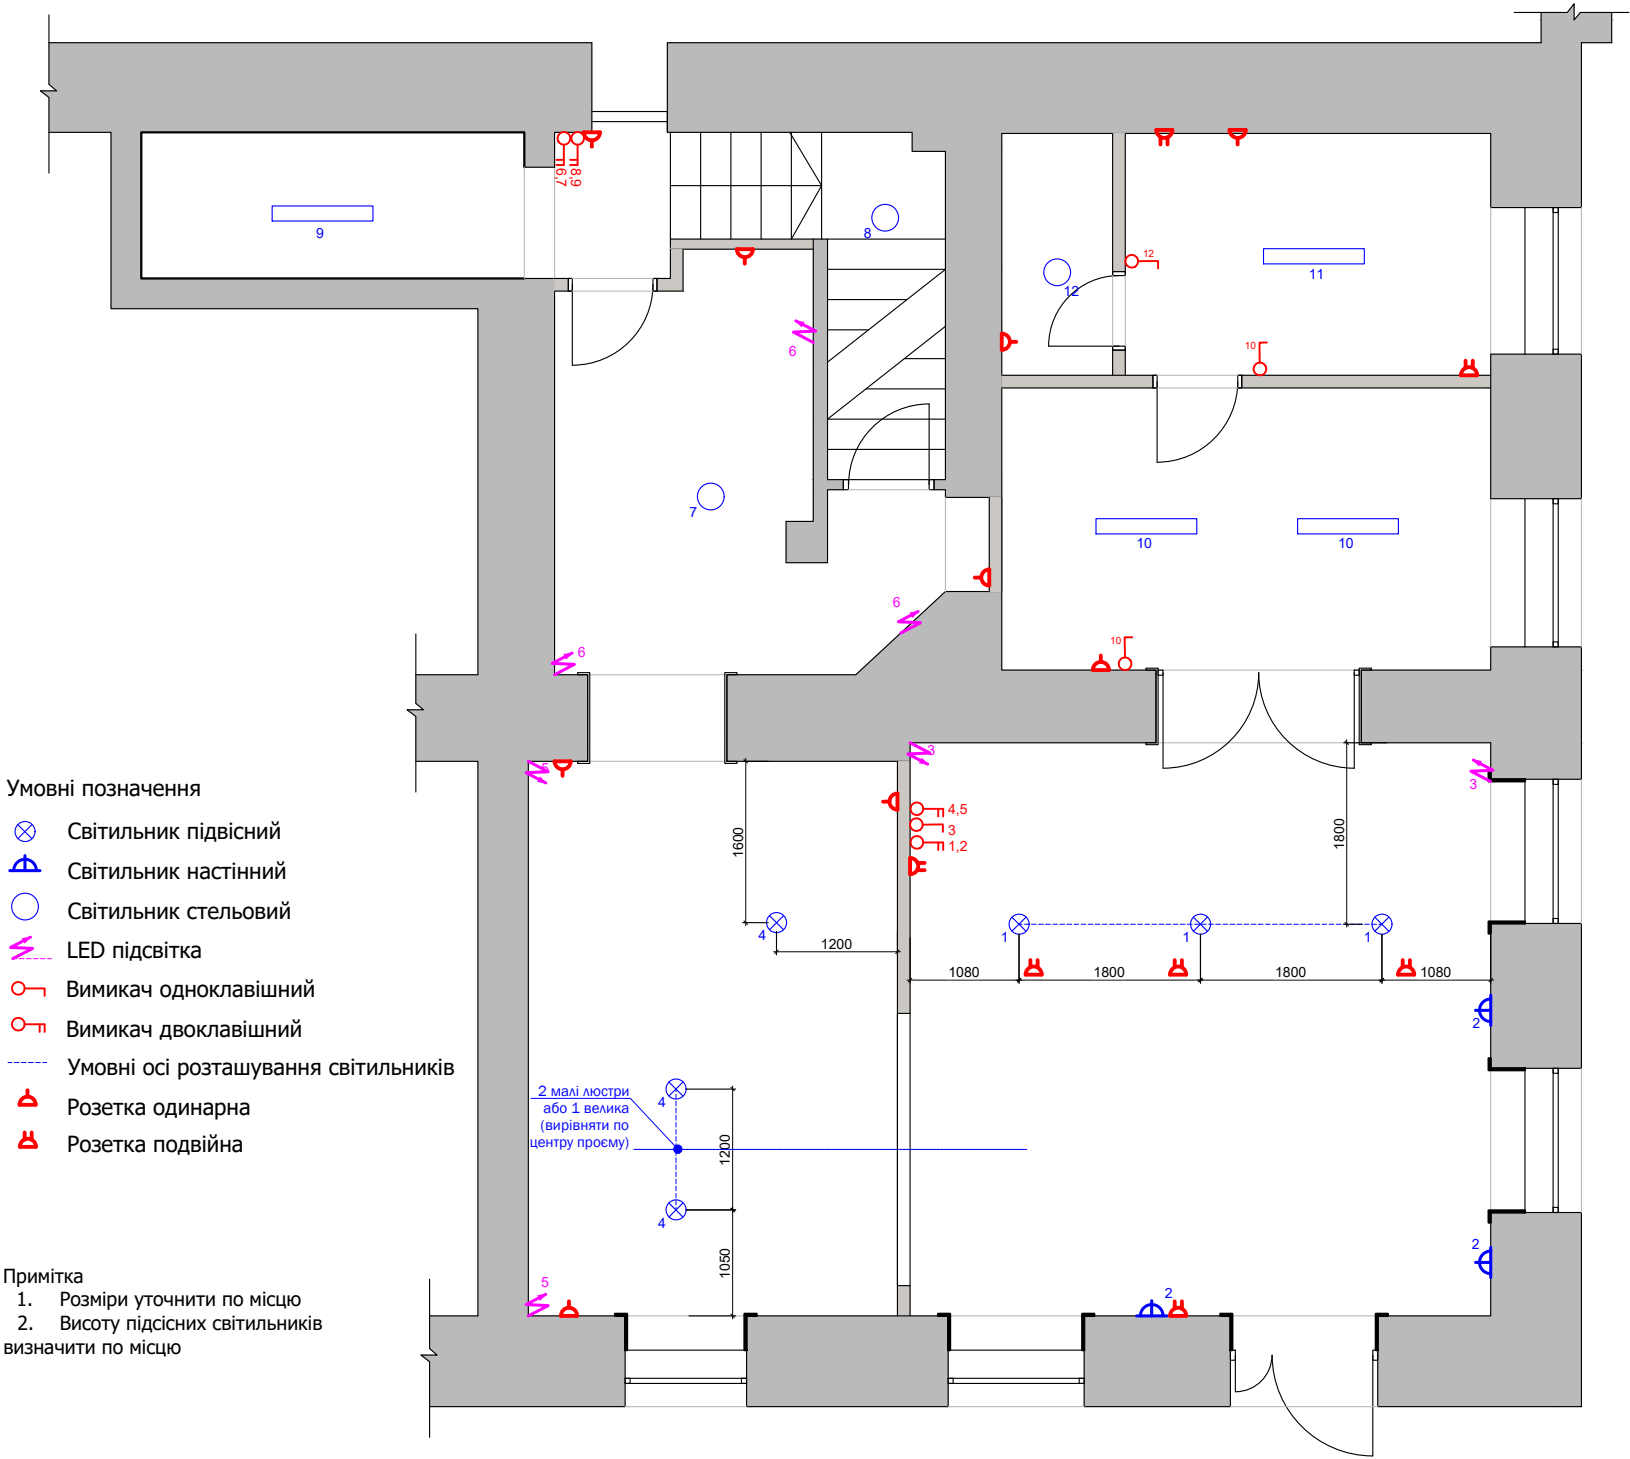

ПРОЕКТ

ПРОЕКТ РЕКОНСТРУКЦІЇ ПРИМІЩЕННЯ

вул. М. Шашкевича, 9
А-2, м. Золочів

НАЗВА АРКУША:

ПЛАН РОЗМІЩЕННЯ ОБЛАДНАННЯ

ДАТА: 12.03.2025

ПРОЕКТ №:

СТАДІЯ	РП
--------	----

ДИЗАЙН:


ПИНДИК НАТАЛЯ

КРЕСЛИВ:

ПИНДИК НАТАЛЯ

МАСШТАБ 1:75

ФОРМАТ ЛИСТА **A3**

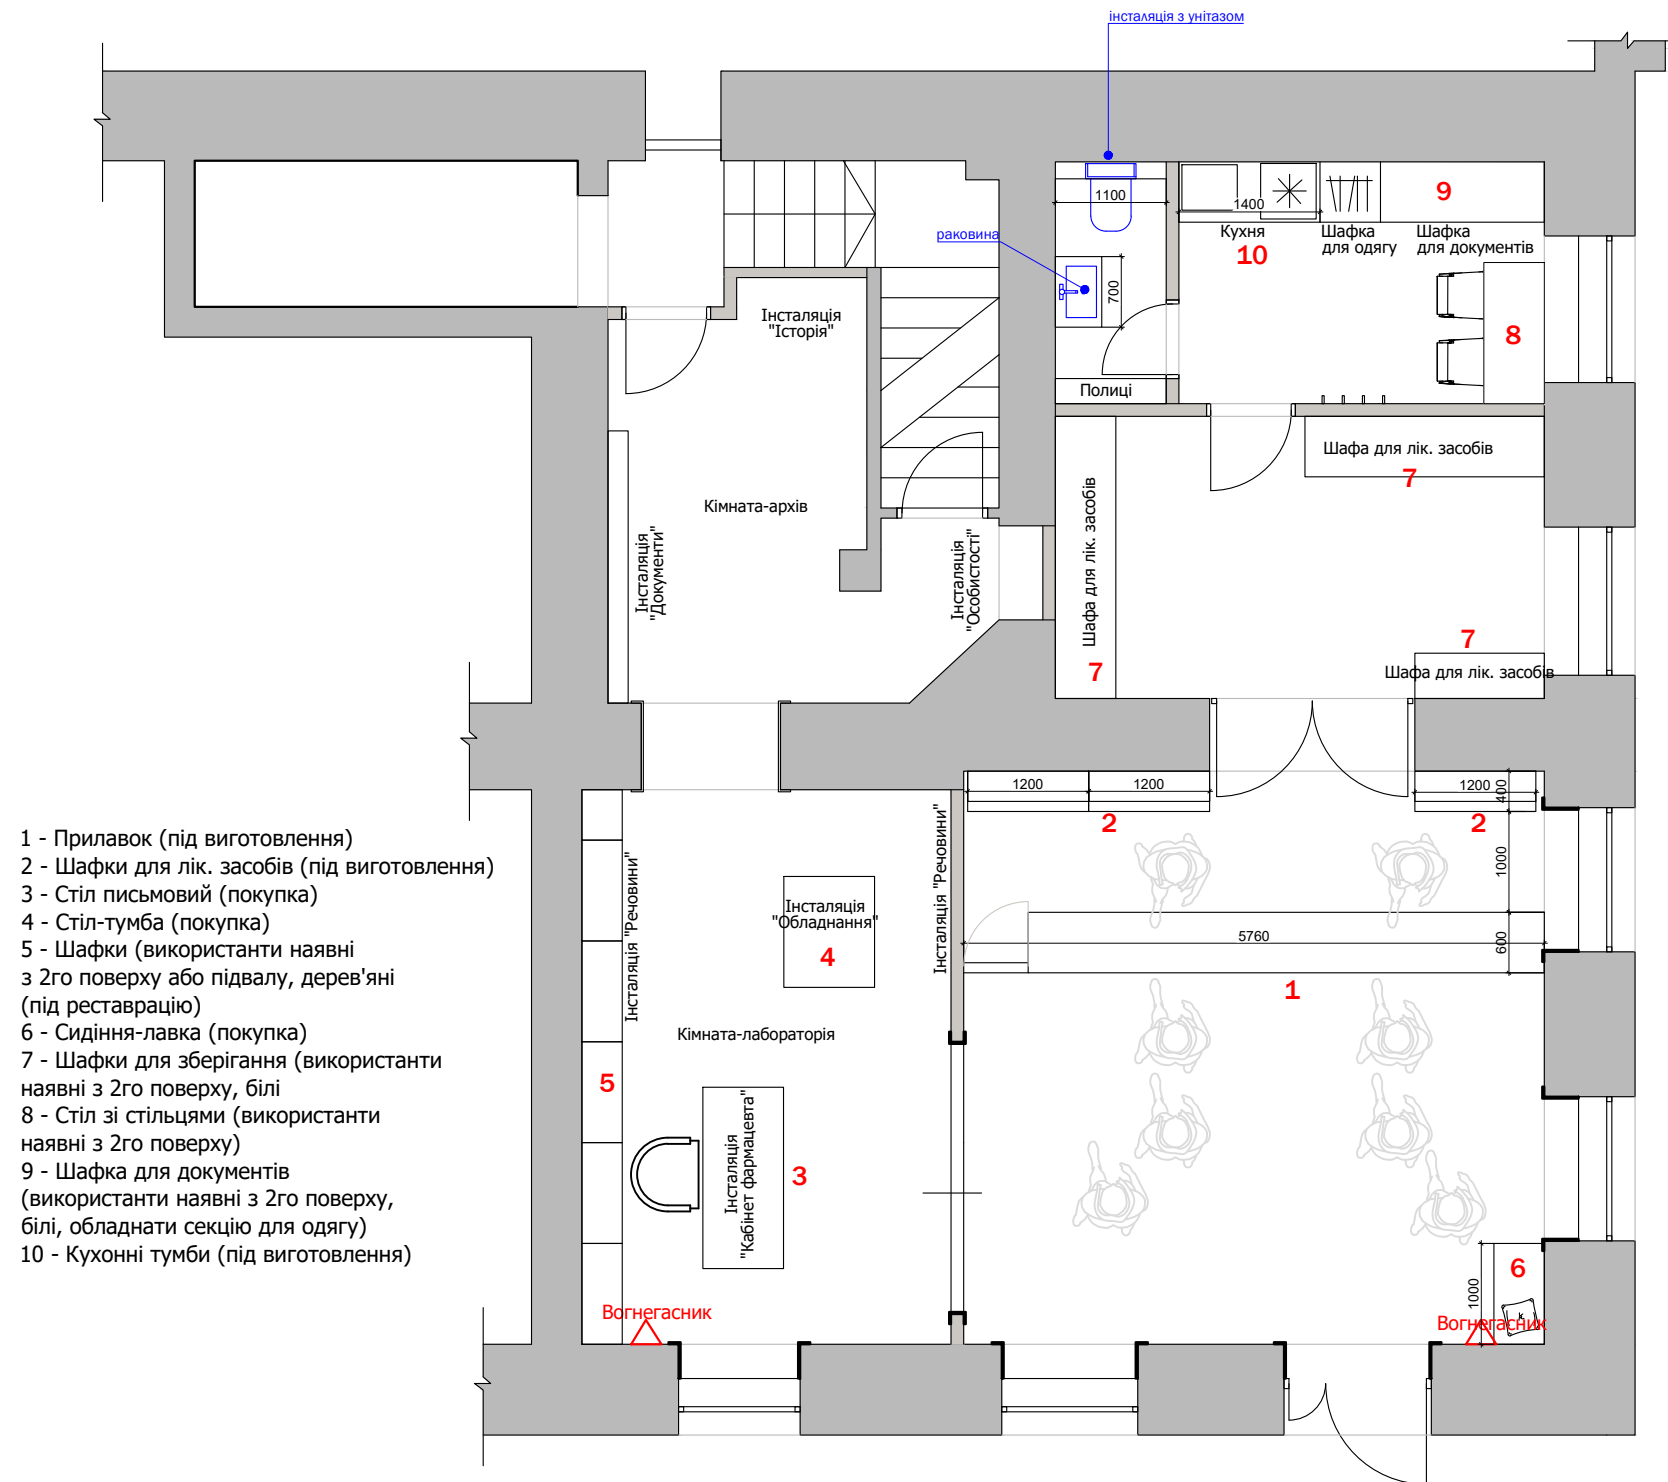

www.behance.net/natalia_pyndyk

+380 967 638 994 - Наталя Пиндик

ПРОЕКТ

ПРОЕКТ
РЕКОНСТРУКЦІЇ
ПРИМІЩЕННЯ

вул. М. Шашкевича, 9
А-2, м. Золочів

НАЗВА АРКУША:

КРЕСЛЕННЯ
ОБЛАДНАННЯ

ДАТА: 12.03.2025

ПРОСКТ №:

СТАДІЯ РП


ДИЗАЙН:
ПИНДИК НАТАЛЯ

КРЕСЛИВ:
ПИНДИК НАТАЛЯ


МАСШТАБ 1:75

ФОРМАТ ЛИСТА А3


1. Прилавок з вітриною

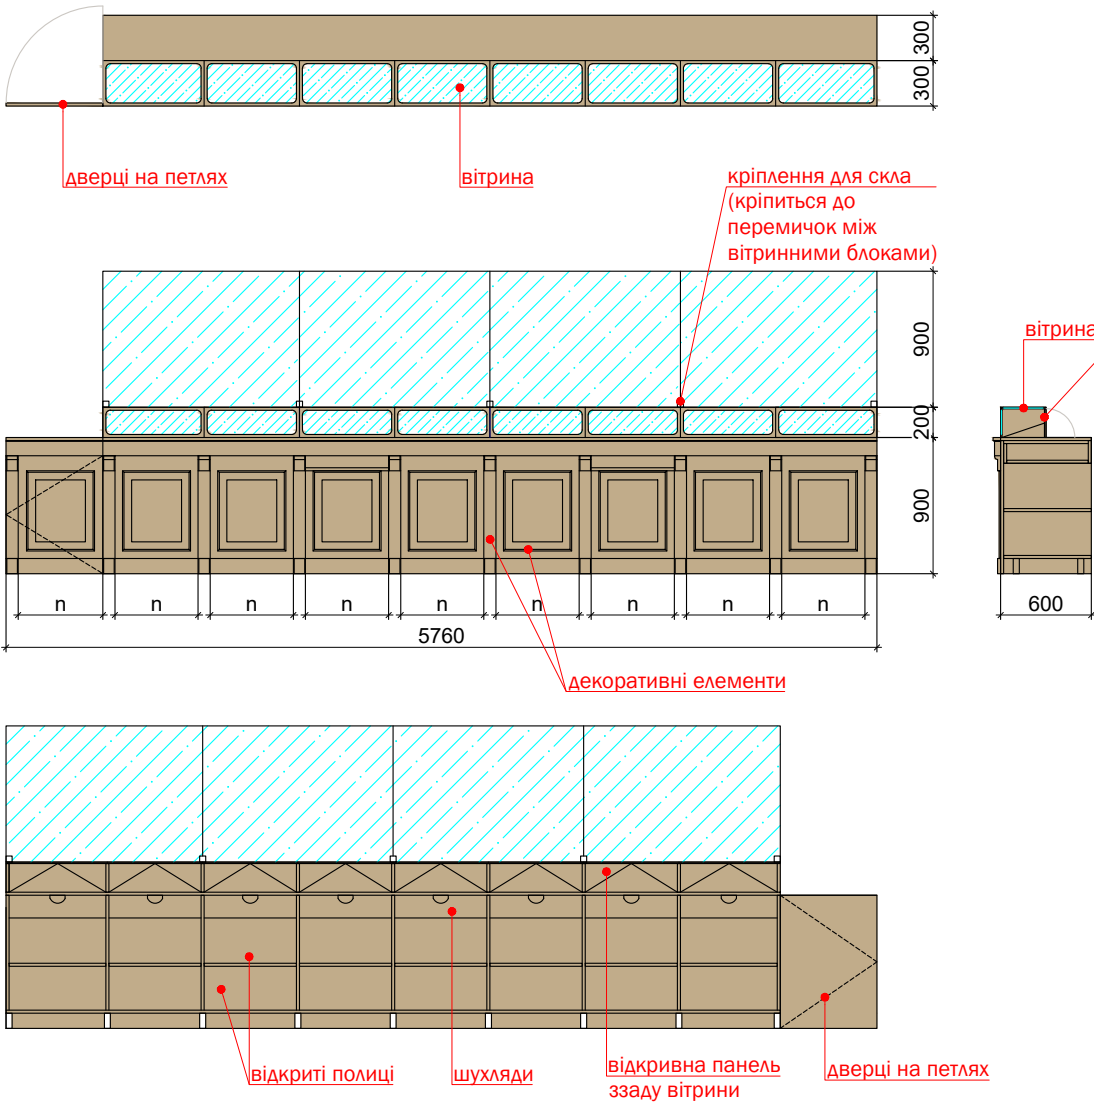

10. Кухня

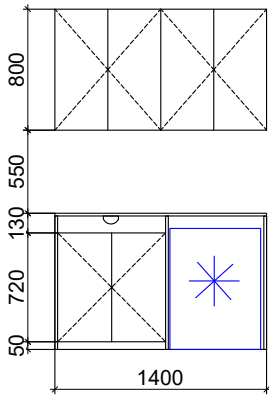

2. Шафки для лік. засобів (3 шт)

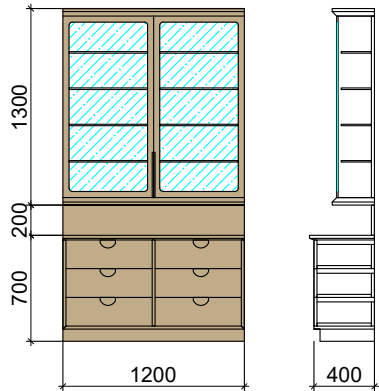

Примітка

1. Розміри уточнити по місцю
2. Висота шафки дорівнює висоті столярних ,

Приклад обробки дерева
(нерівномірне покриття маслом, мат)

