
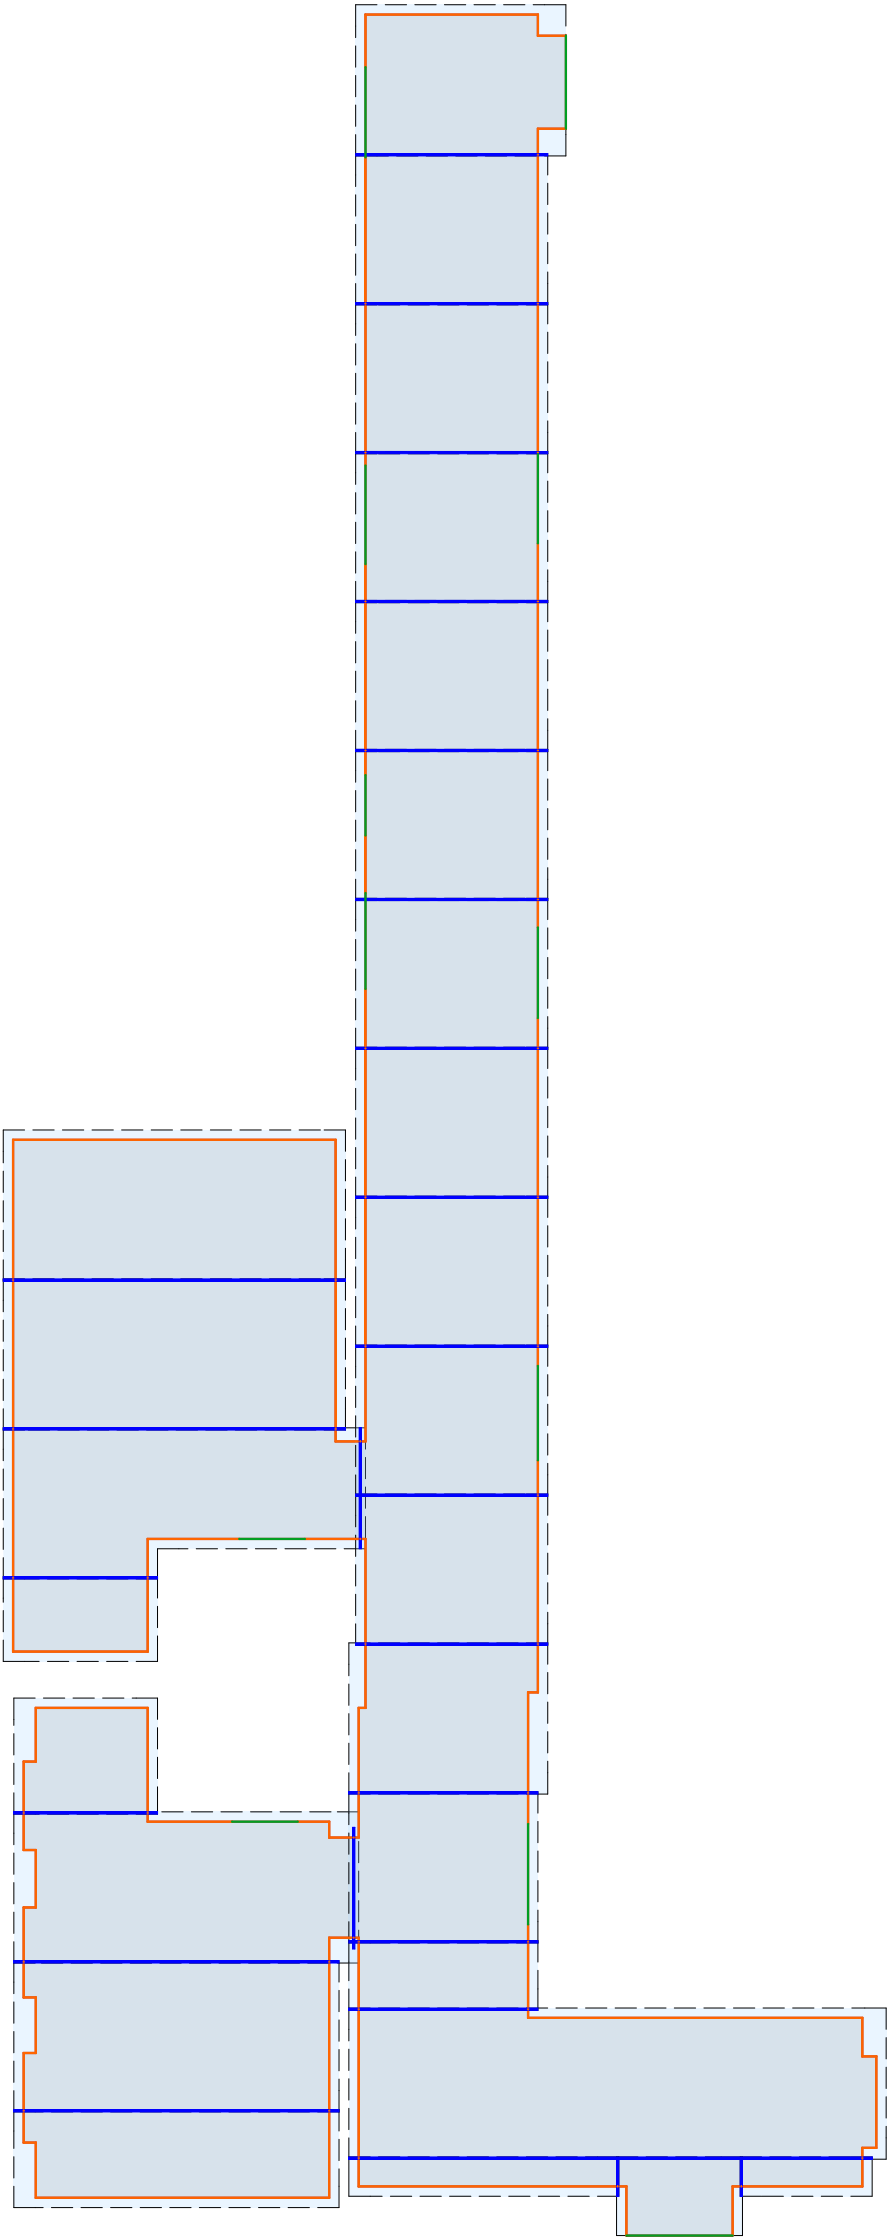


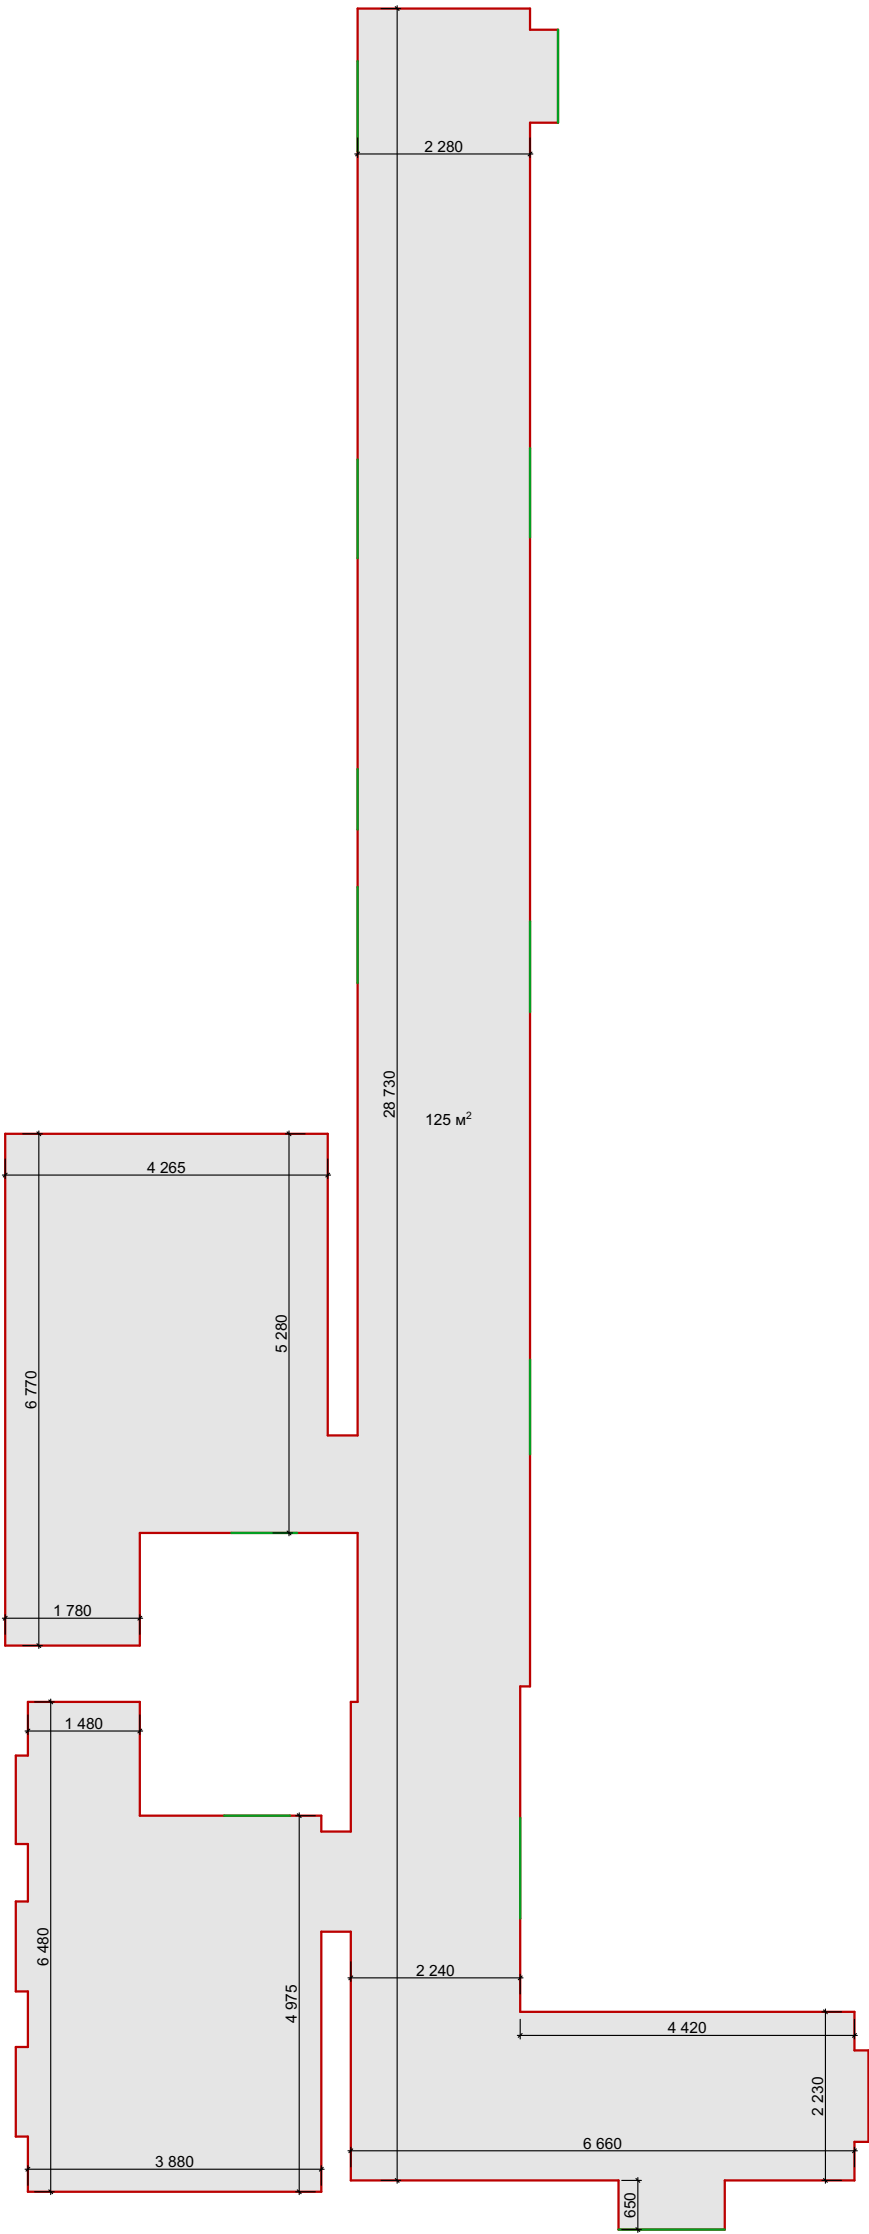

Shera Essence		- $S_{\text{площа прим.}} = 125 \text{ m}^2$
		- $S_{\text{площа ПВХ покр. (рулонка 2 м)}} = 147,2 \text{ m}^2$
		- $L_{\text{плінтус EL / галтель 25x25 мм}} = 105 \text{ м/п}$ (враховано запас 5 м/п)
		- $L_{\text{Погонаж шнур спайки}} = 80 \text{ м/п}$ (враховано запас 3 м/п)